




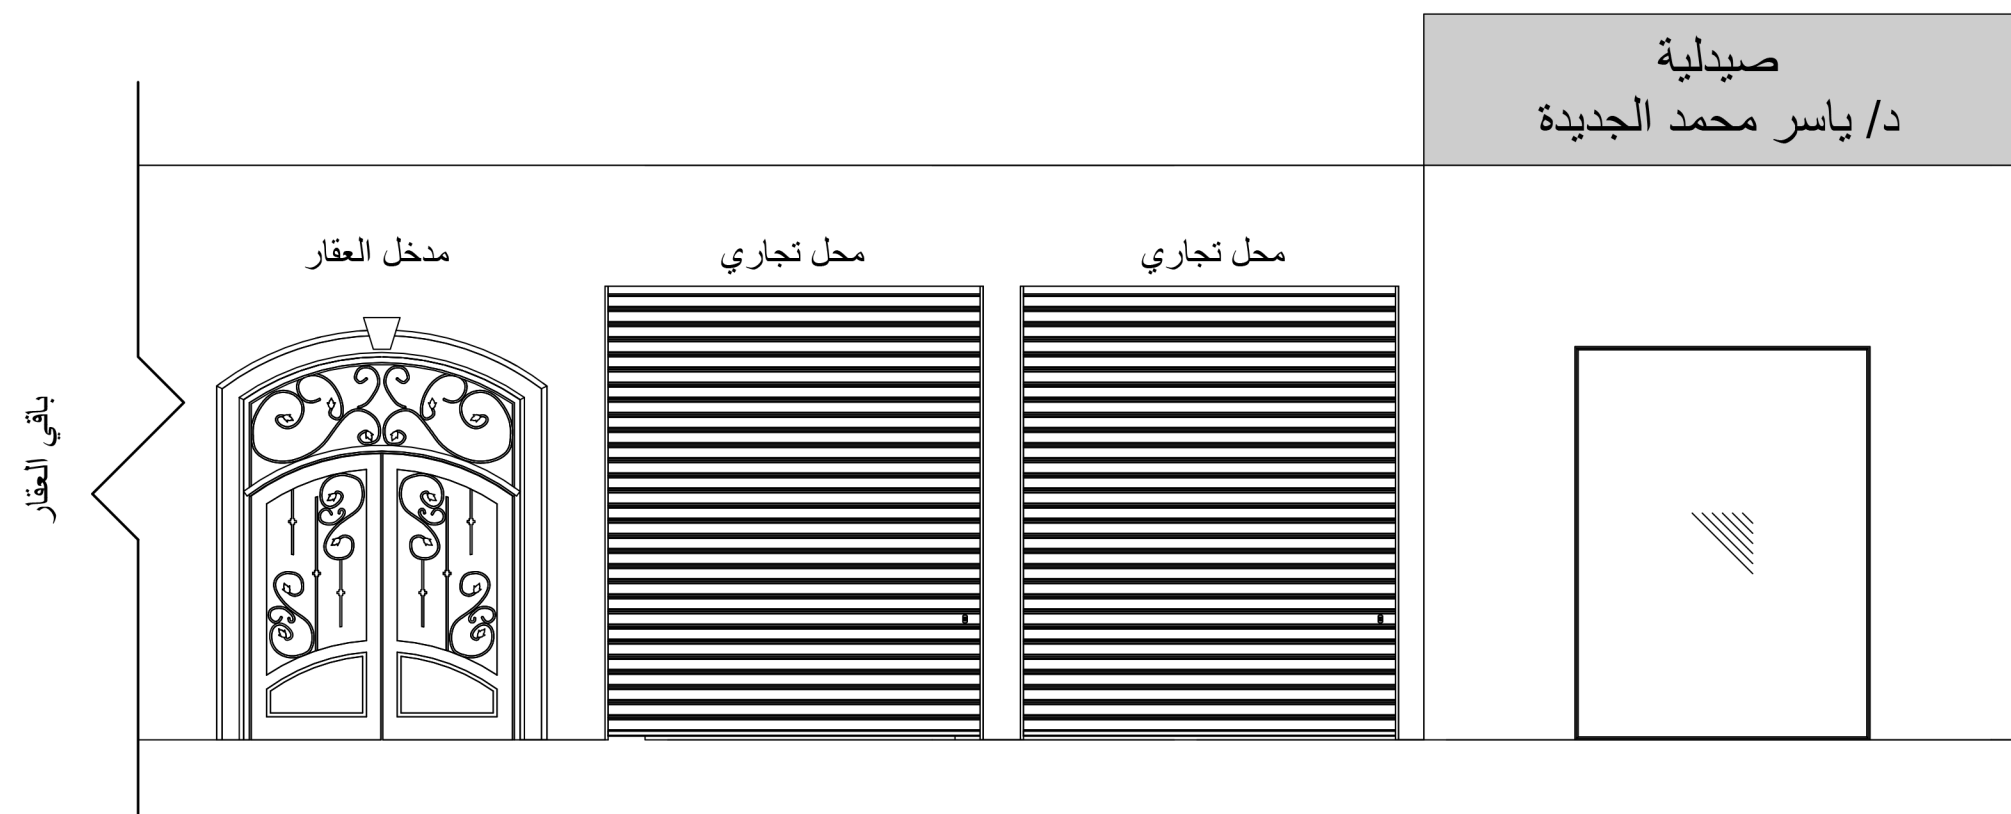


2 واجهة جانبية
1 : 50

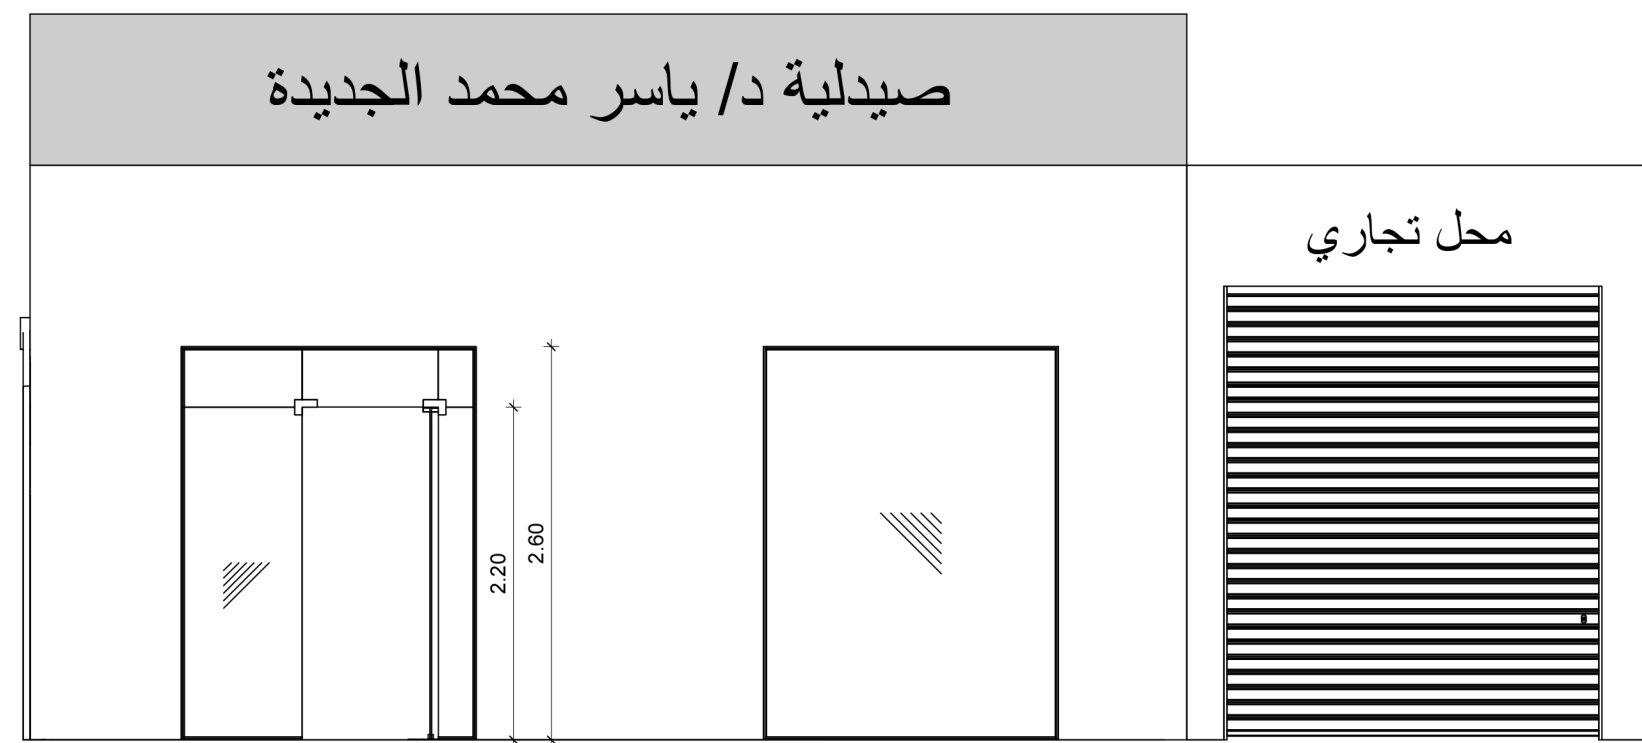


3 واجهة أمامية (على شارع المصنع)
1 : 50

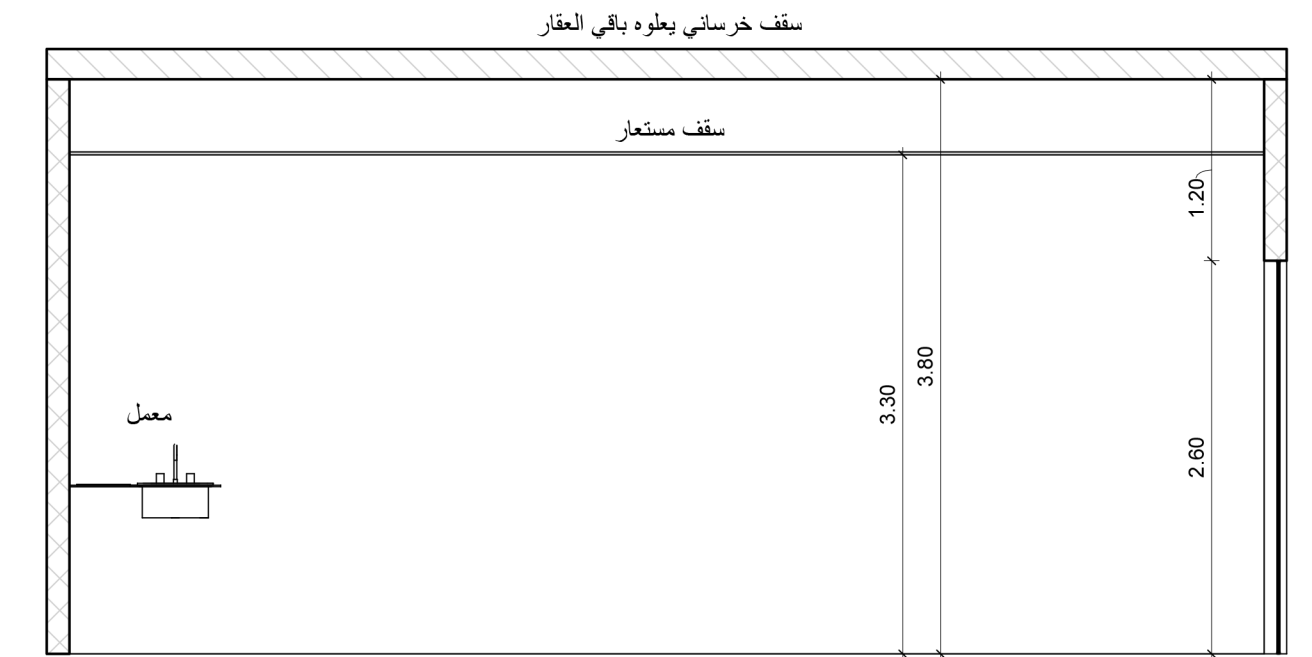

4 قطاع رأسي
1 : 50

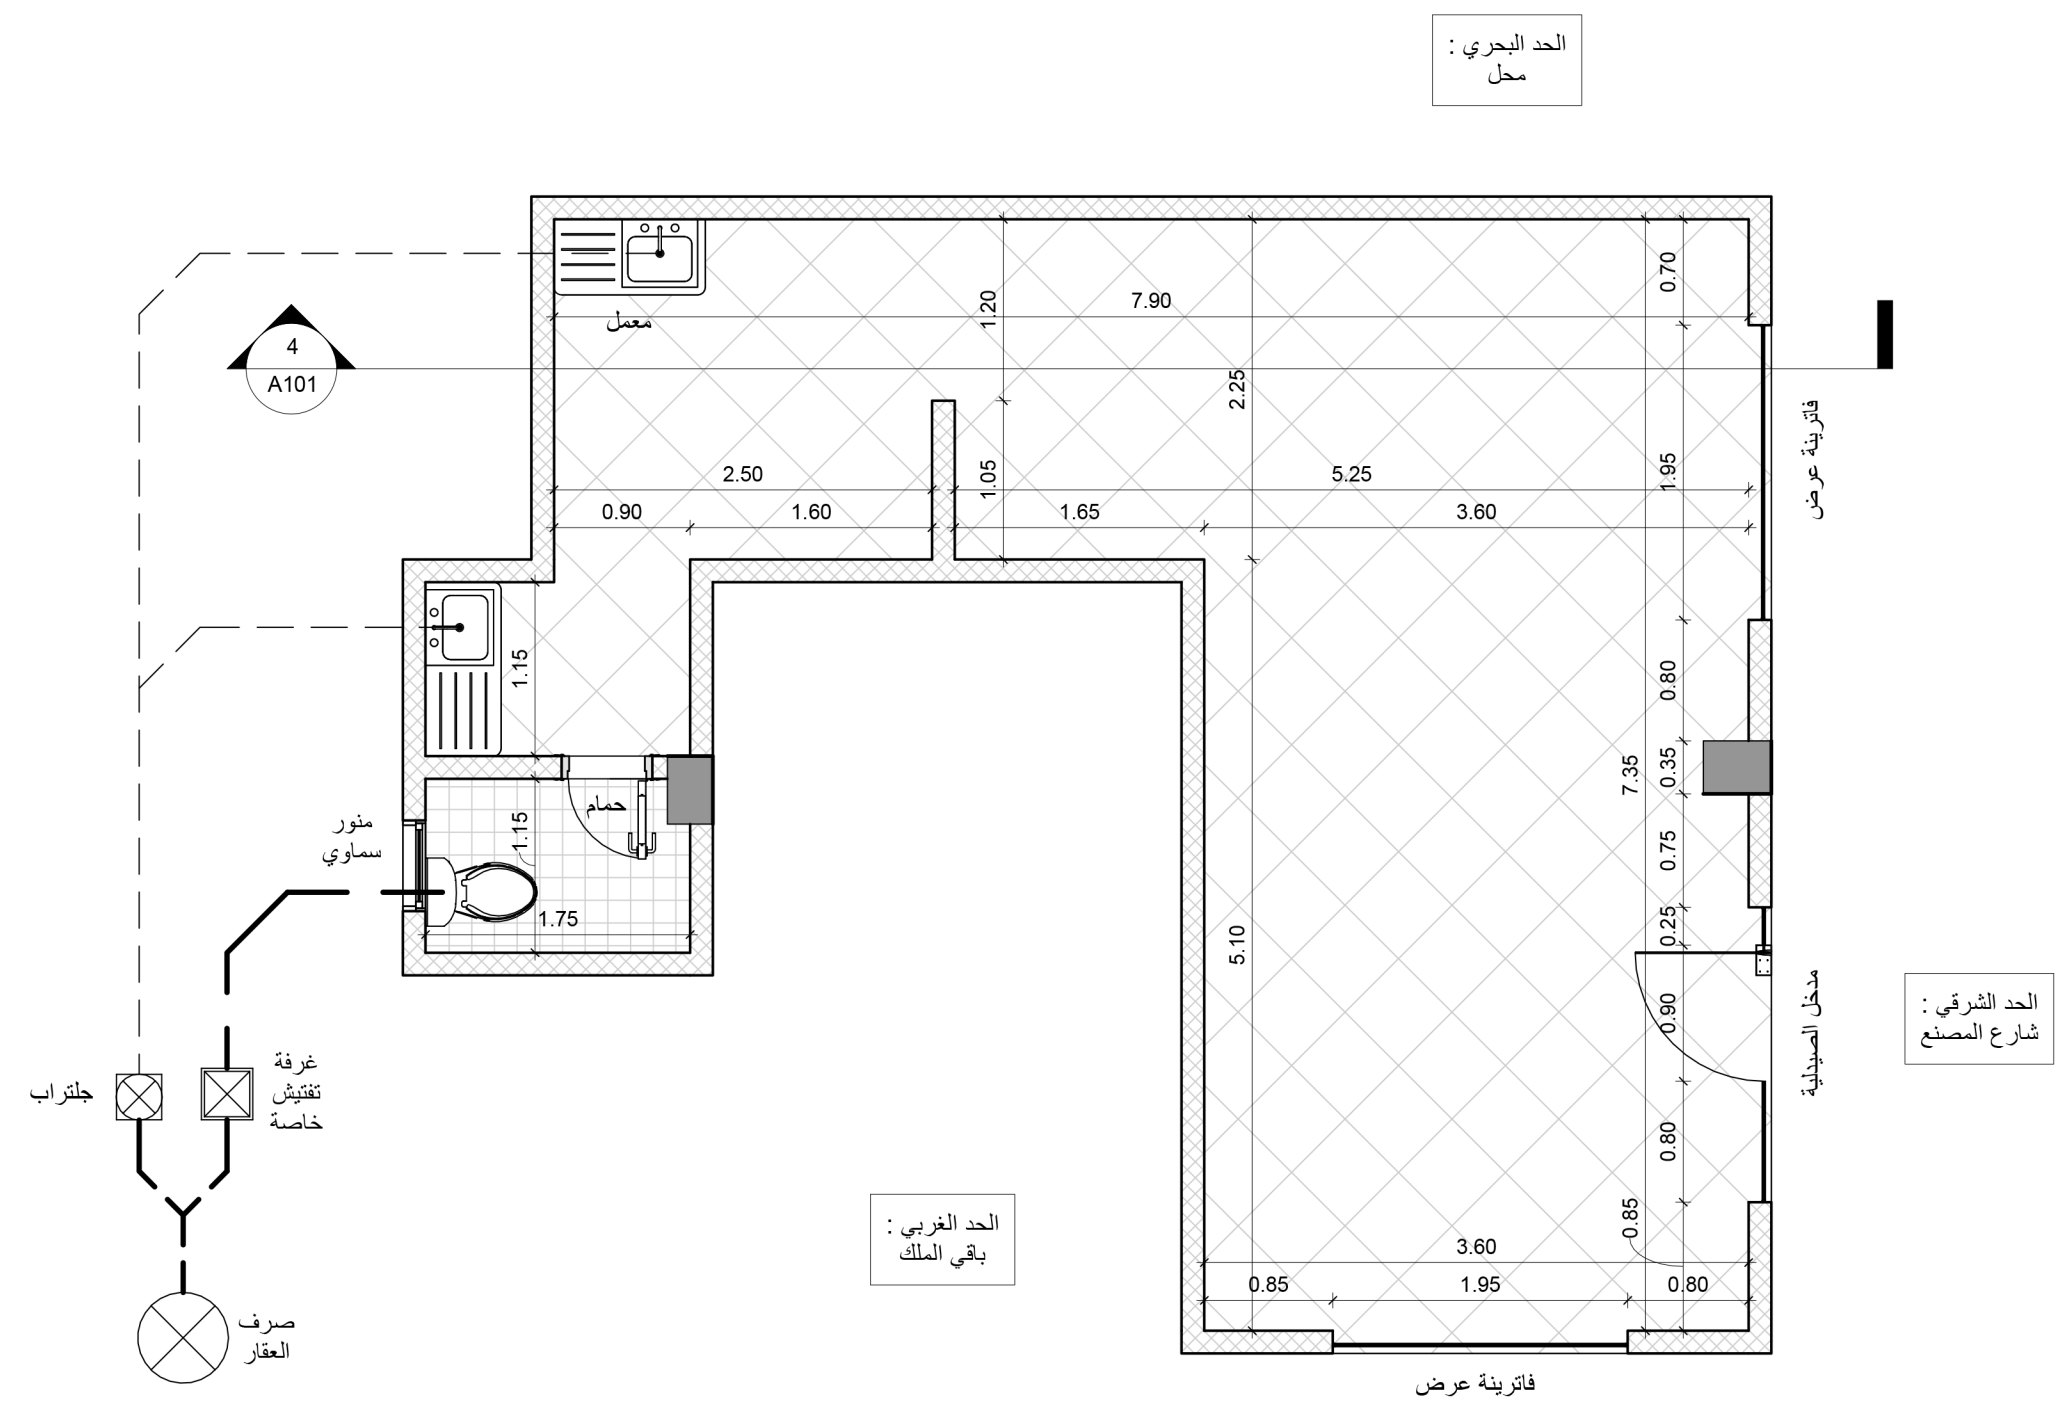


1 مسقط أفقي
1 : 50

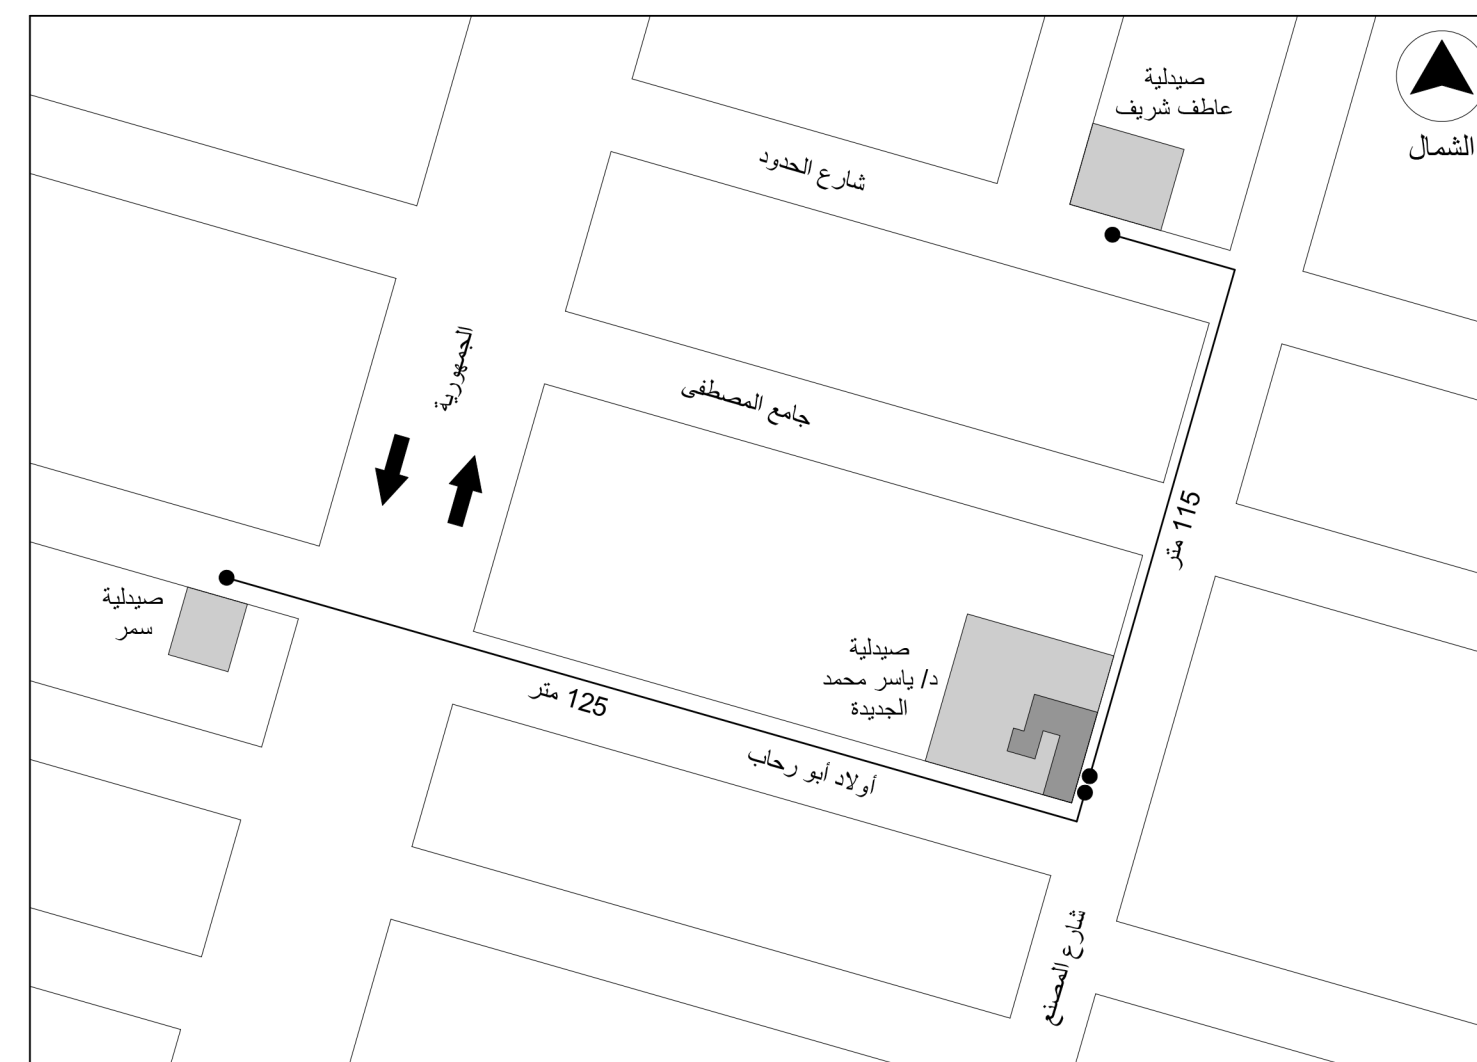


5 الموقع العام
1 : 1000


صاحب الصيدلية	صاحب الصيدلية
اسم الصيدلية	صيدلية د/ ياسر محمد الجديدة
المساحة	40.00 م ²
العنوان	
مقياس الرسم	50:1
	
www.emocrete.com 01014490054	

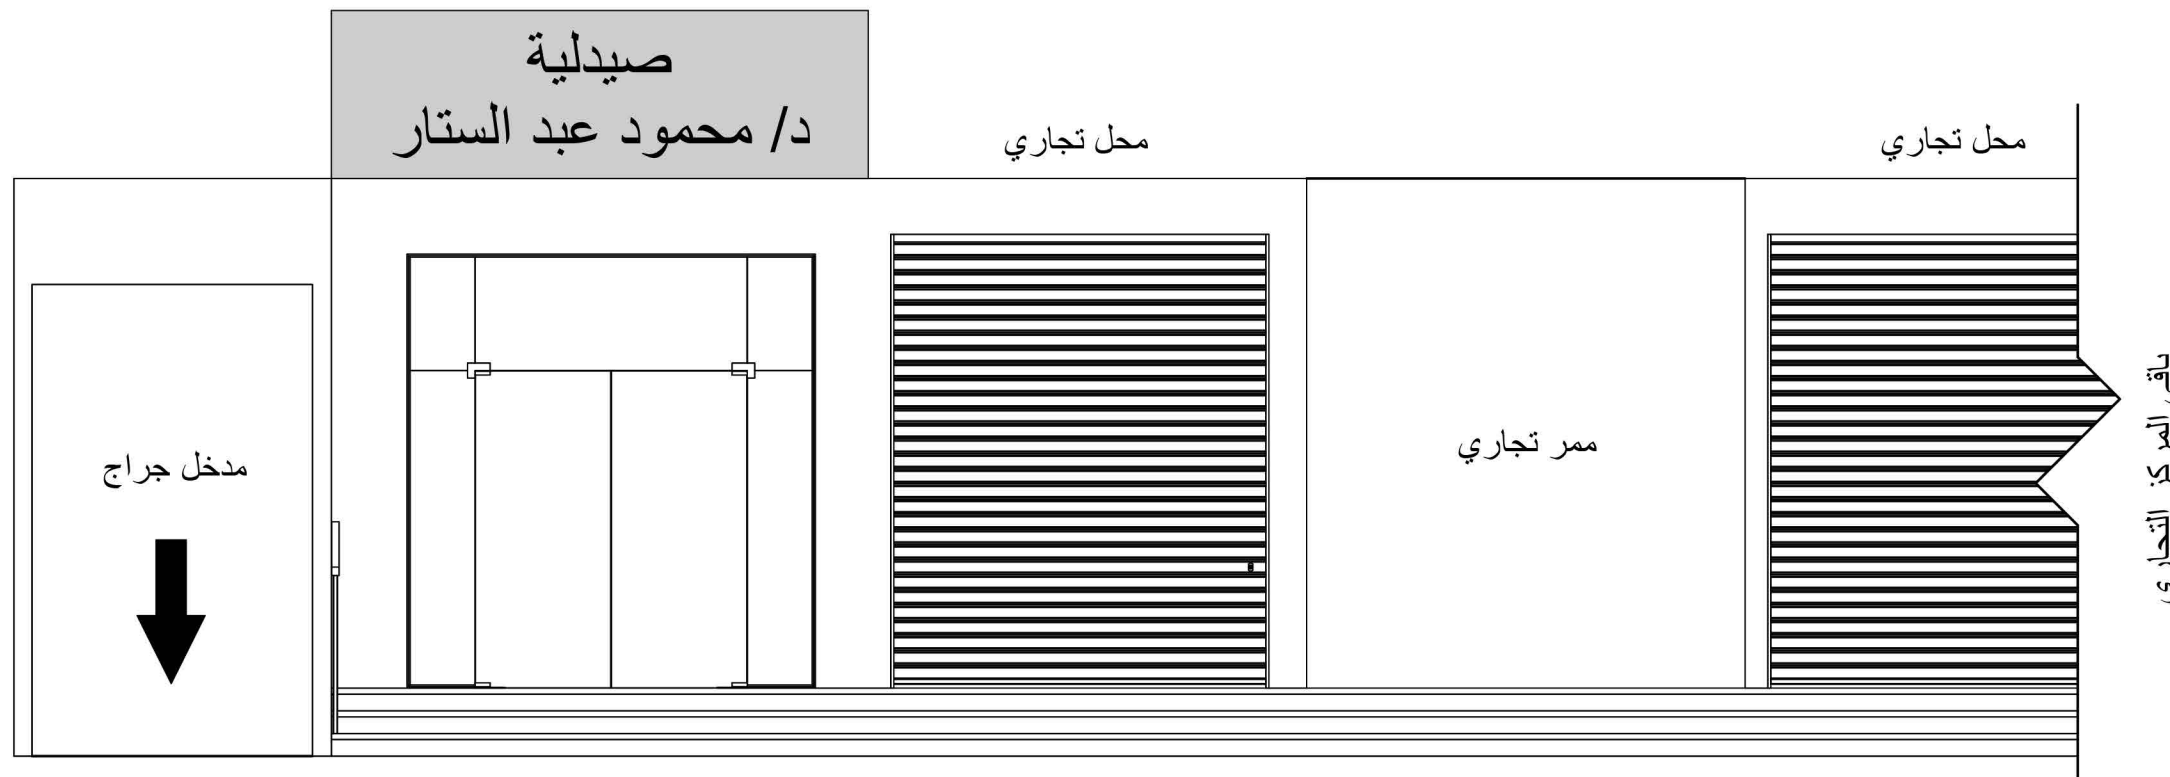


2 واجهة أمامية
1 : 50

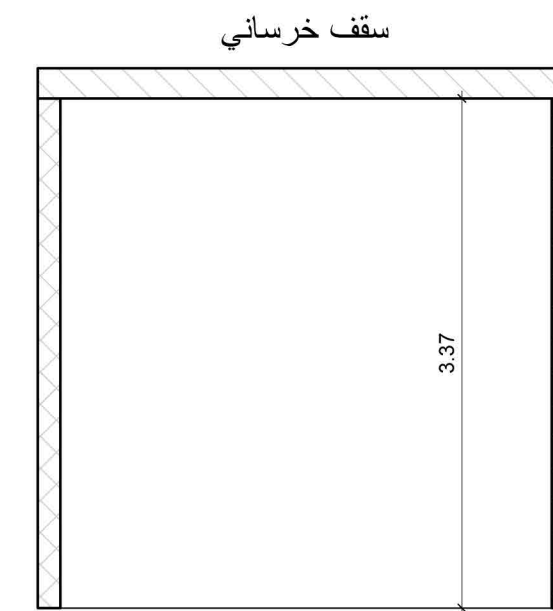

3 قطاع رأسي
1 : 50

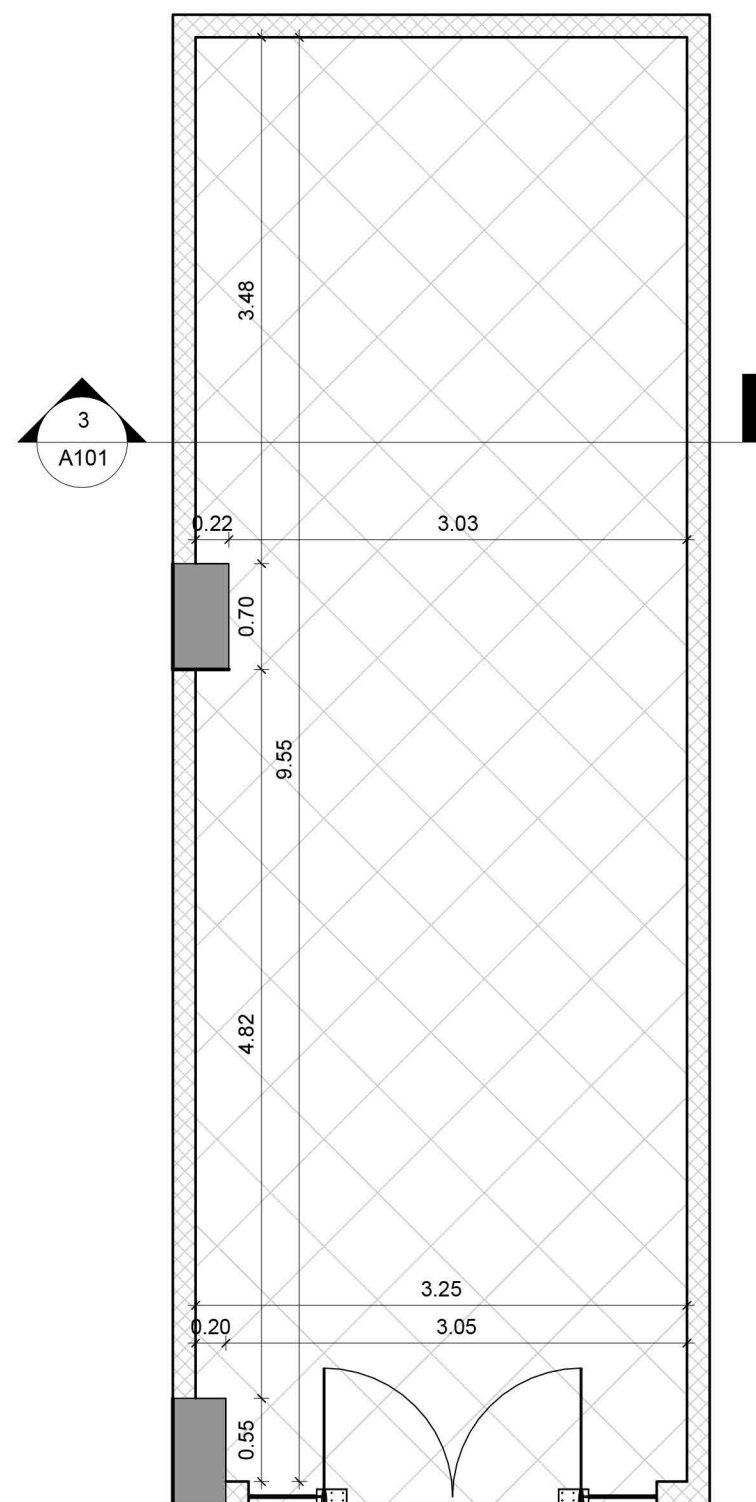


1 مسقط أفقي
1 : 50

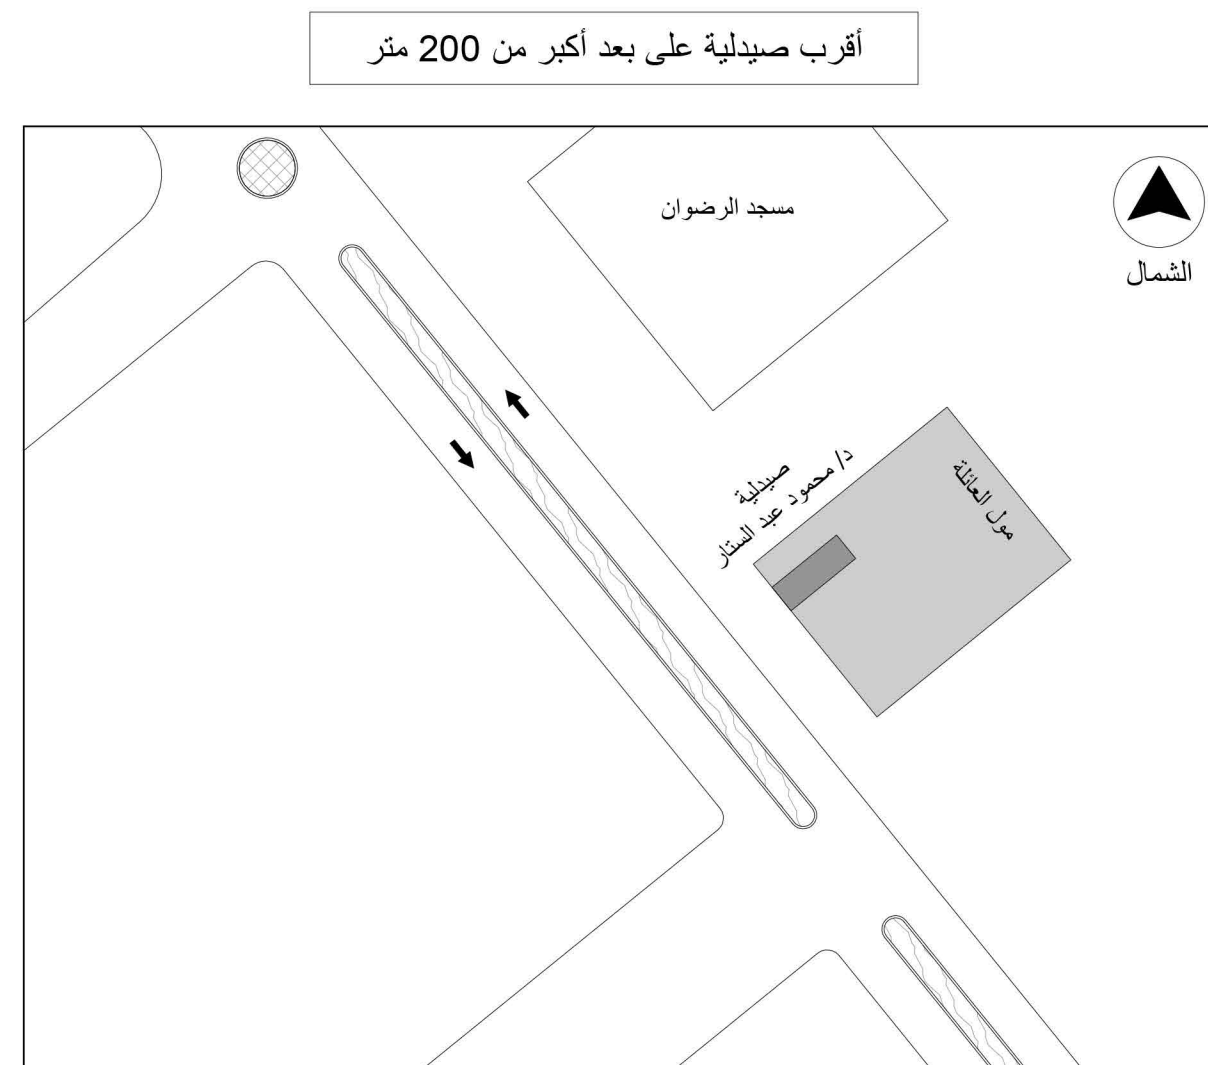


4 الموقع العام
1 : 1000


صاحب الصيدلية	صيدلية د/ محمود عبد الستار
اسم الصيدلية	31.20 م2
المساحة	العنوان
مقياس الرسم	50:1
www.emocrete.com 01014490054	

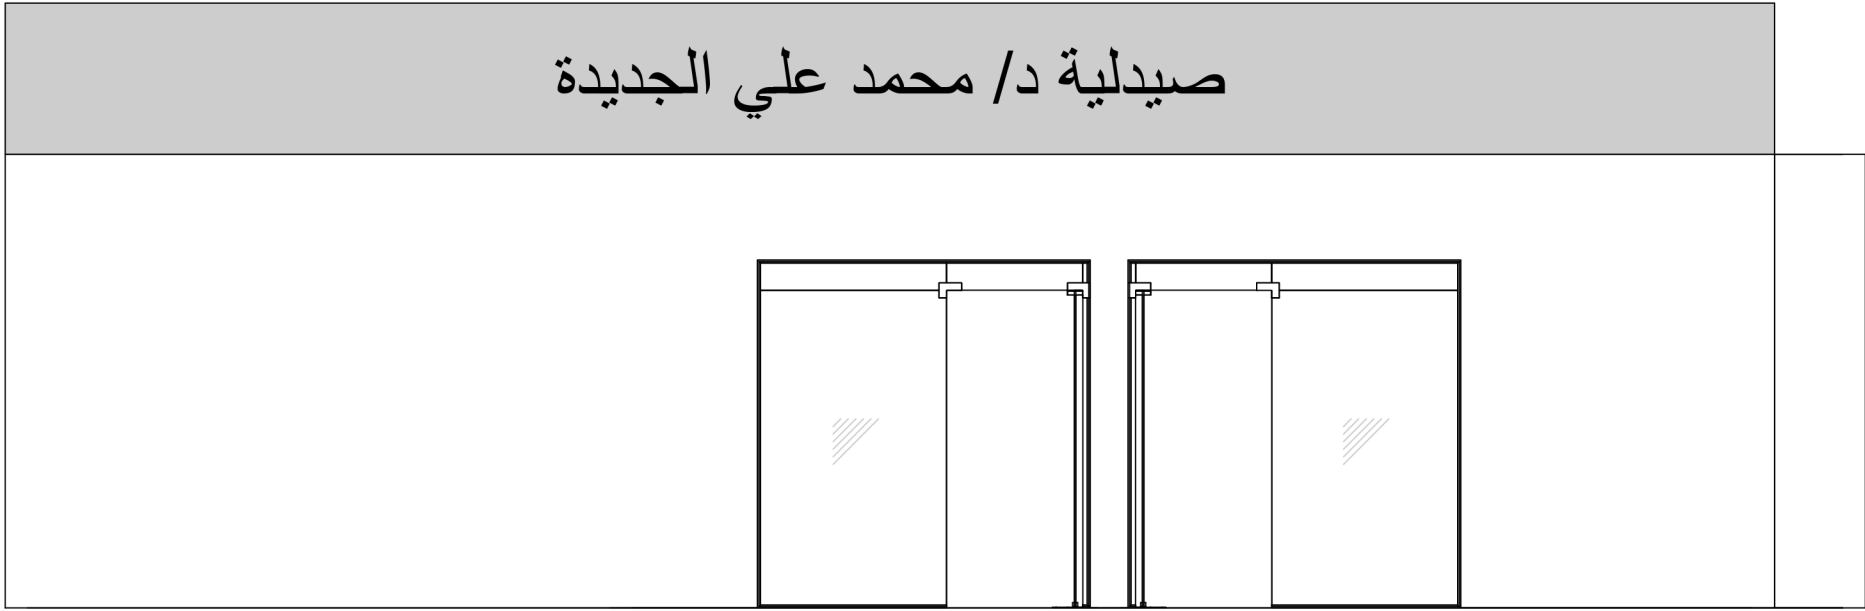


1 واجهة أمامية
1 : 50

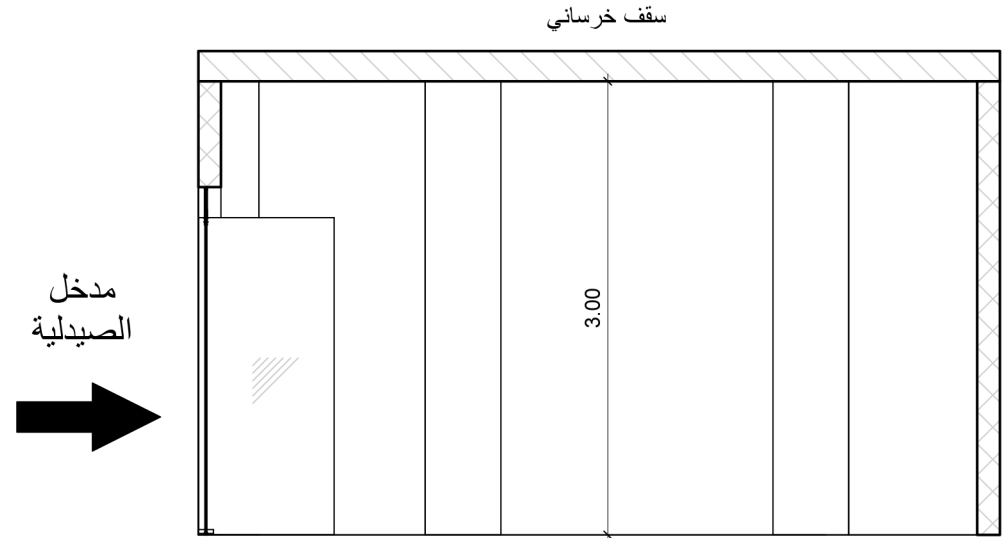

3 قطاع رأسي
1 : 50

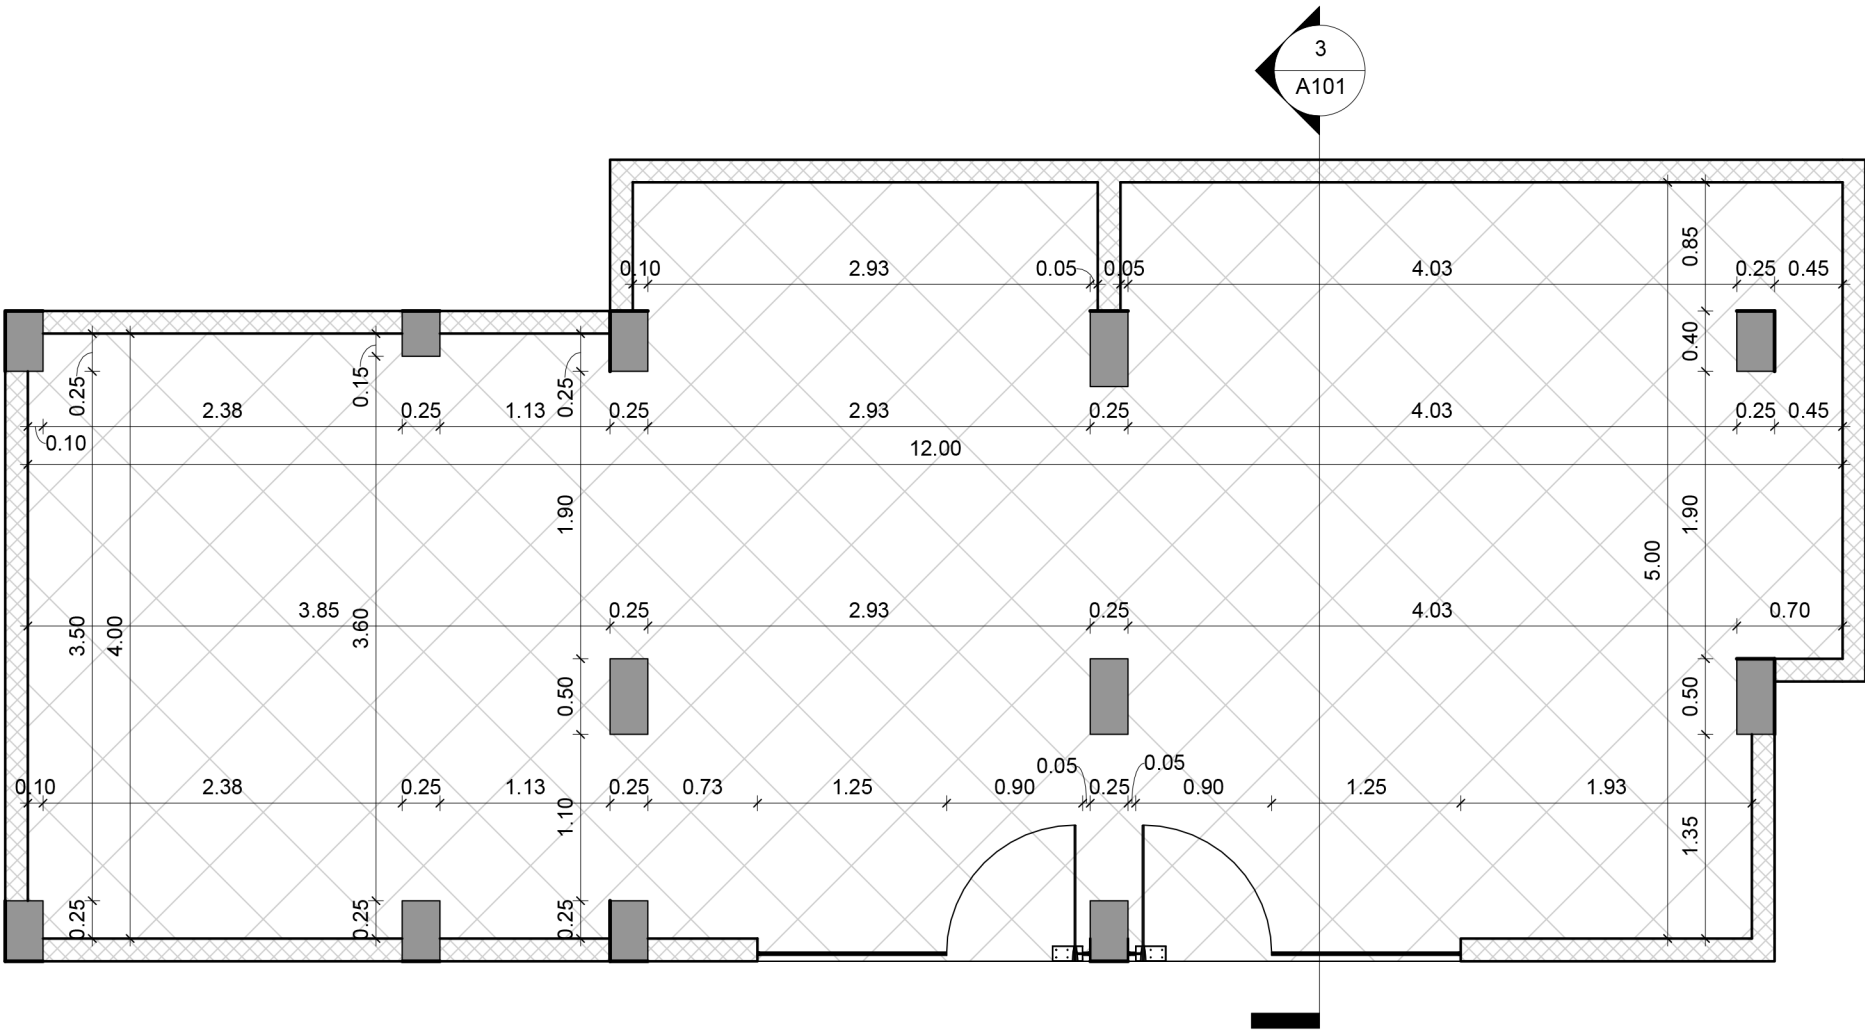


2 مسقط أفقي
1 : 50

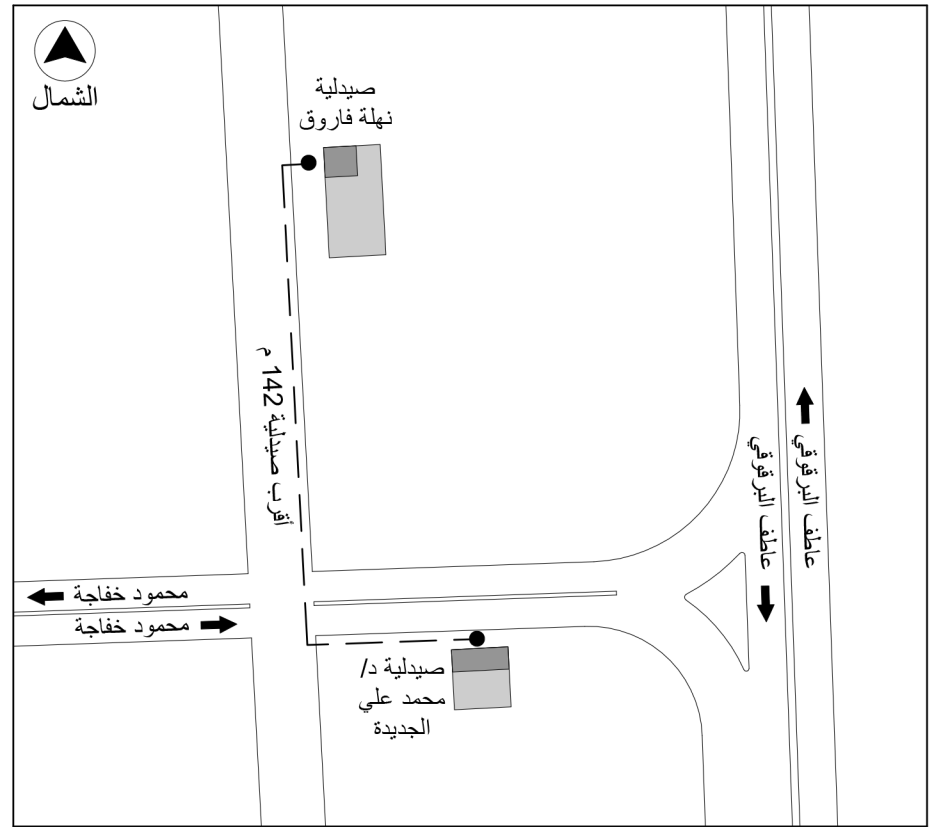


4 الموقع العام
1 : 2000


صاحب الصيدلية	
اسم الصيدلية	صيدلية د/ محمد علي الجديدة
المساحة	55.60 م ²
العنوان	
مقياس الرسم	50:1
	
www.emocrete.com 01014490054	

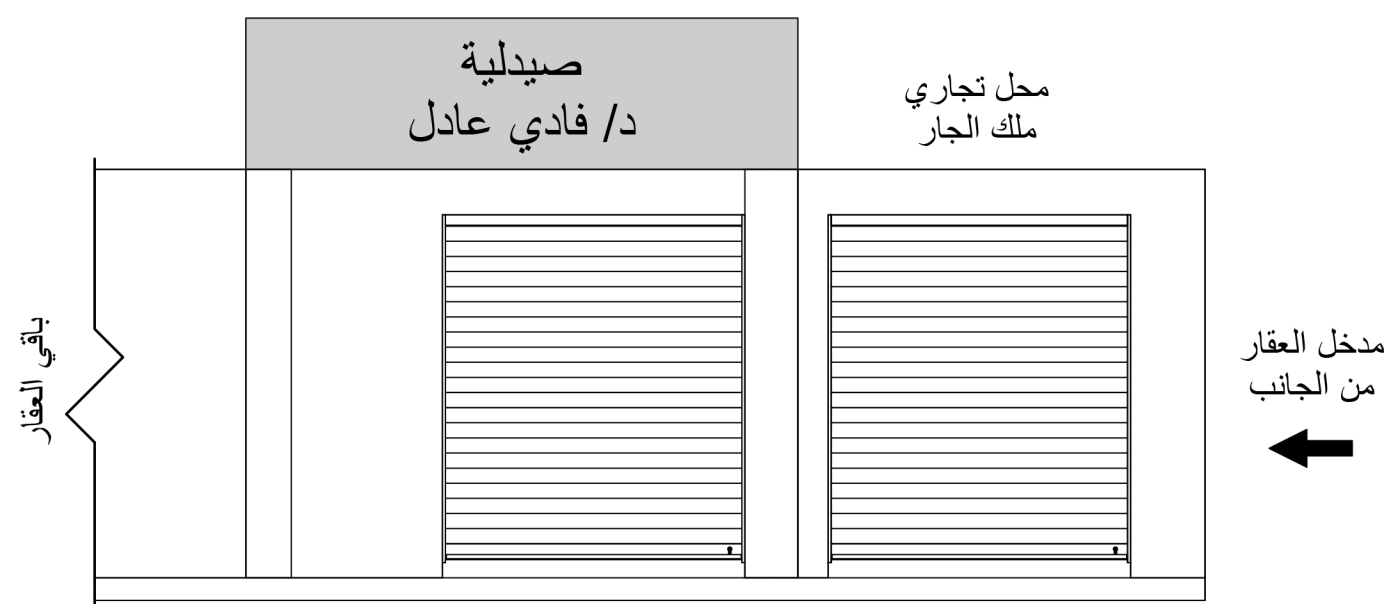


2 واجهة أمامية
1 : 50

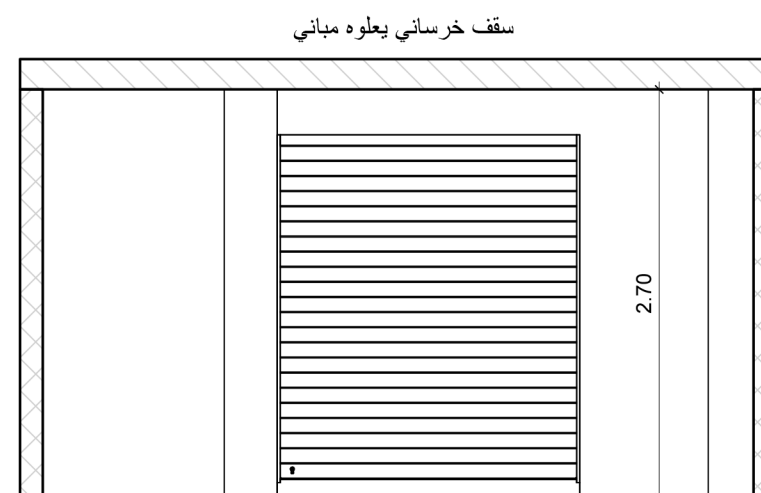

3 قطاع رأسي
1 : 50




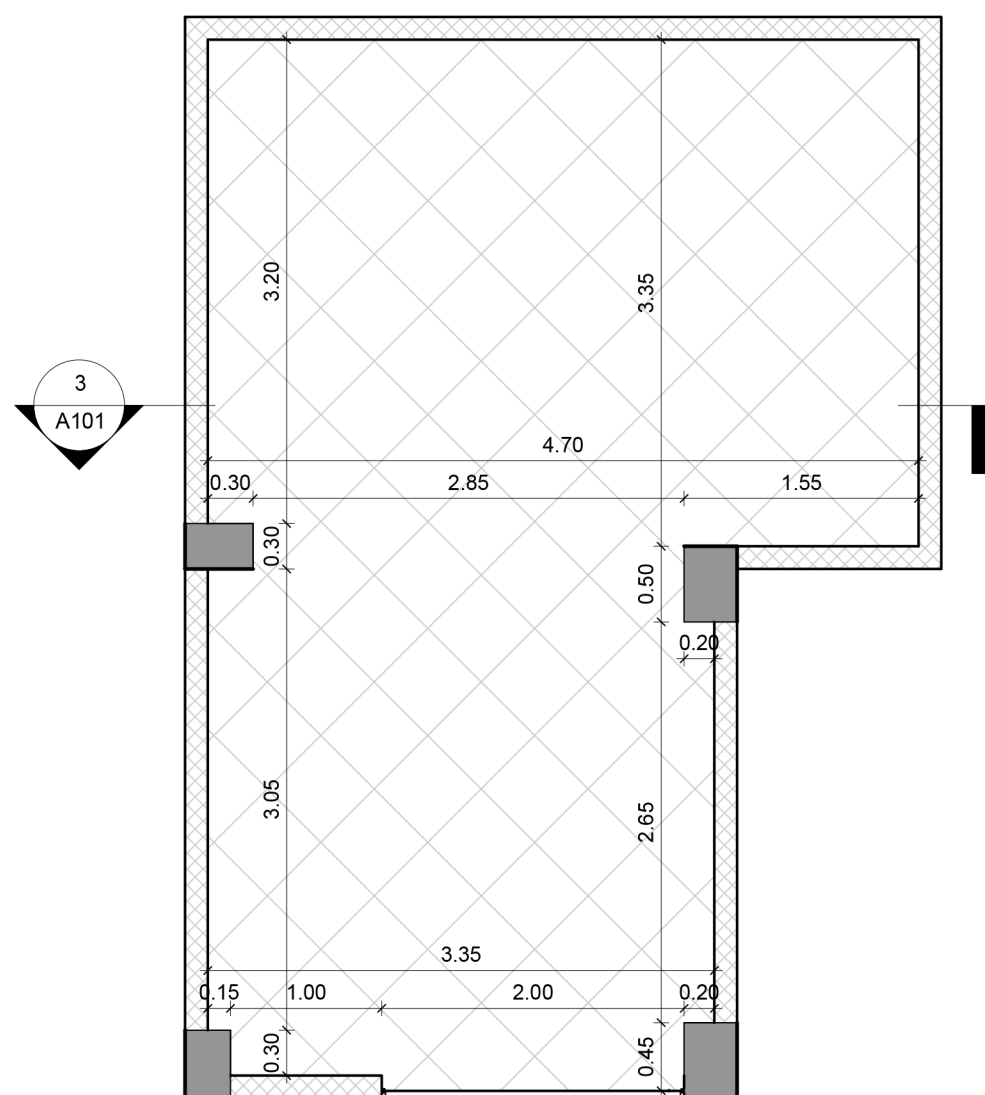


1 مسقط أفقي
1 : 50

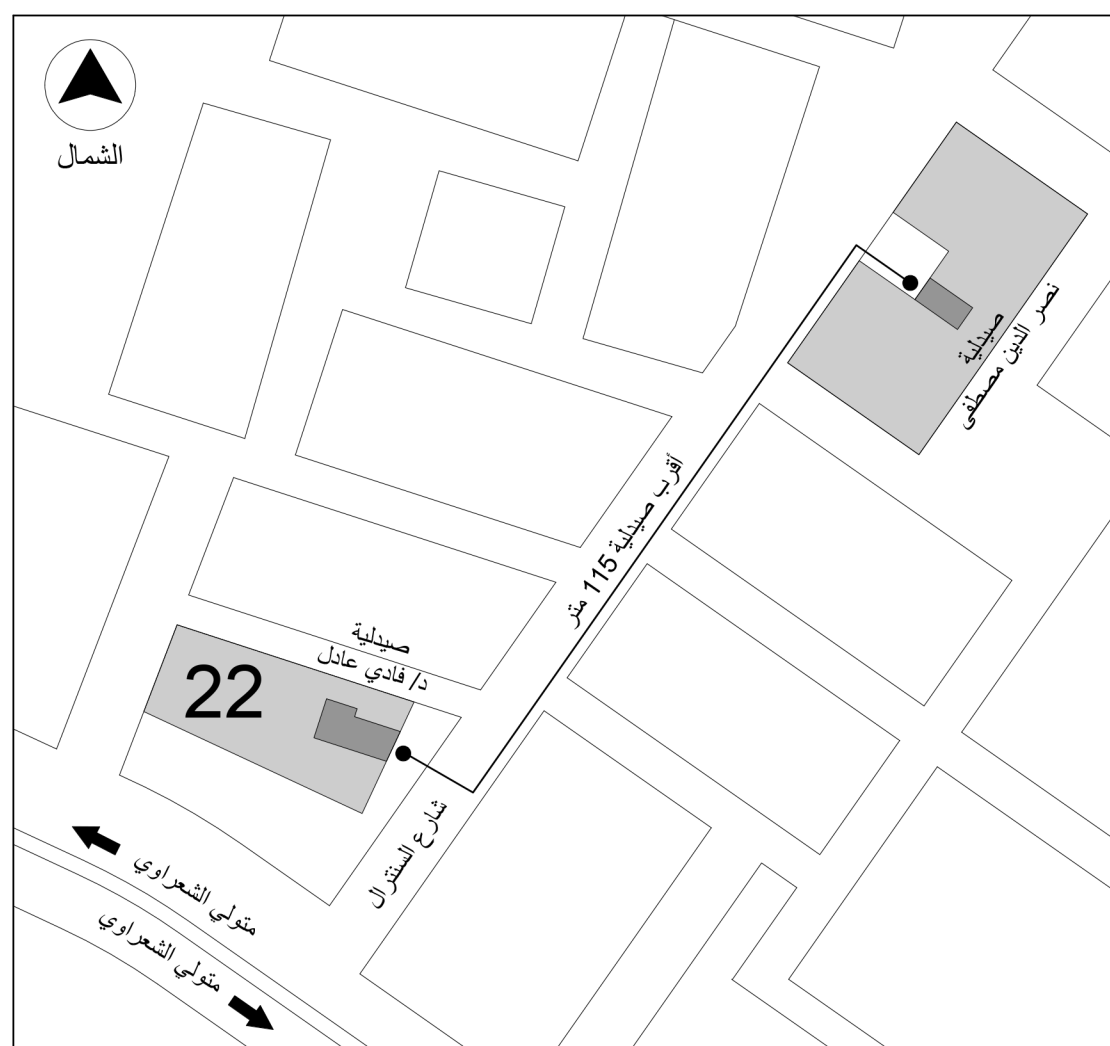


4 الموقع العام
1 : 1000


صاحب الصيدلية	
اسم الصيدلية	صيدلية د/ فادي عادل
المساحة	27.45 م ²
العنوان	
مقياس الرسم	50:1
	
www.emocrete.com 01014490054	

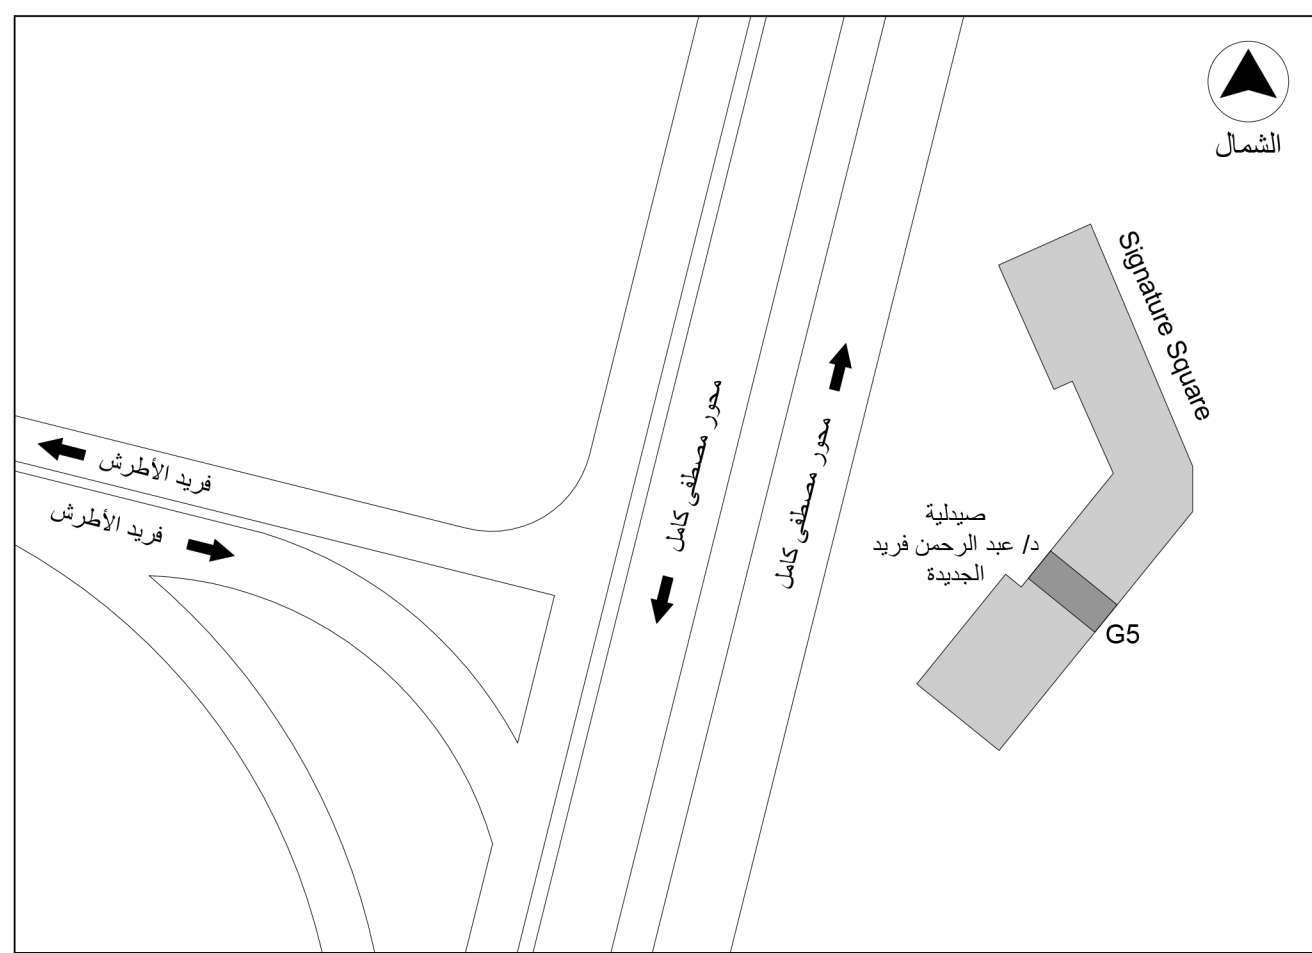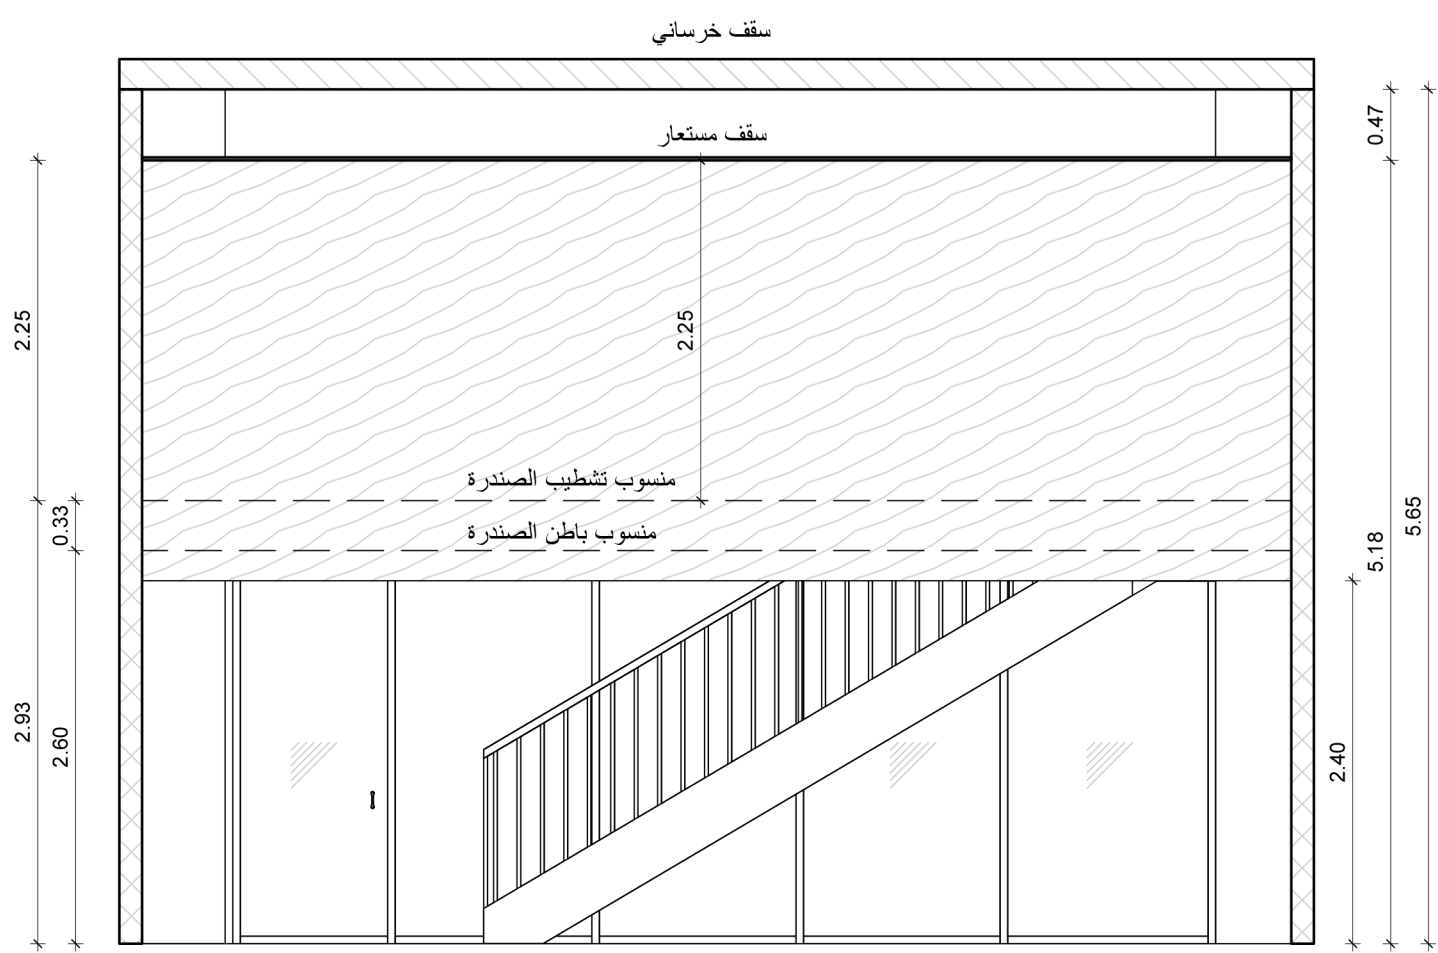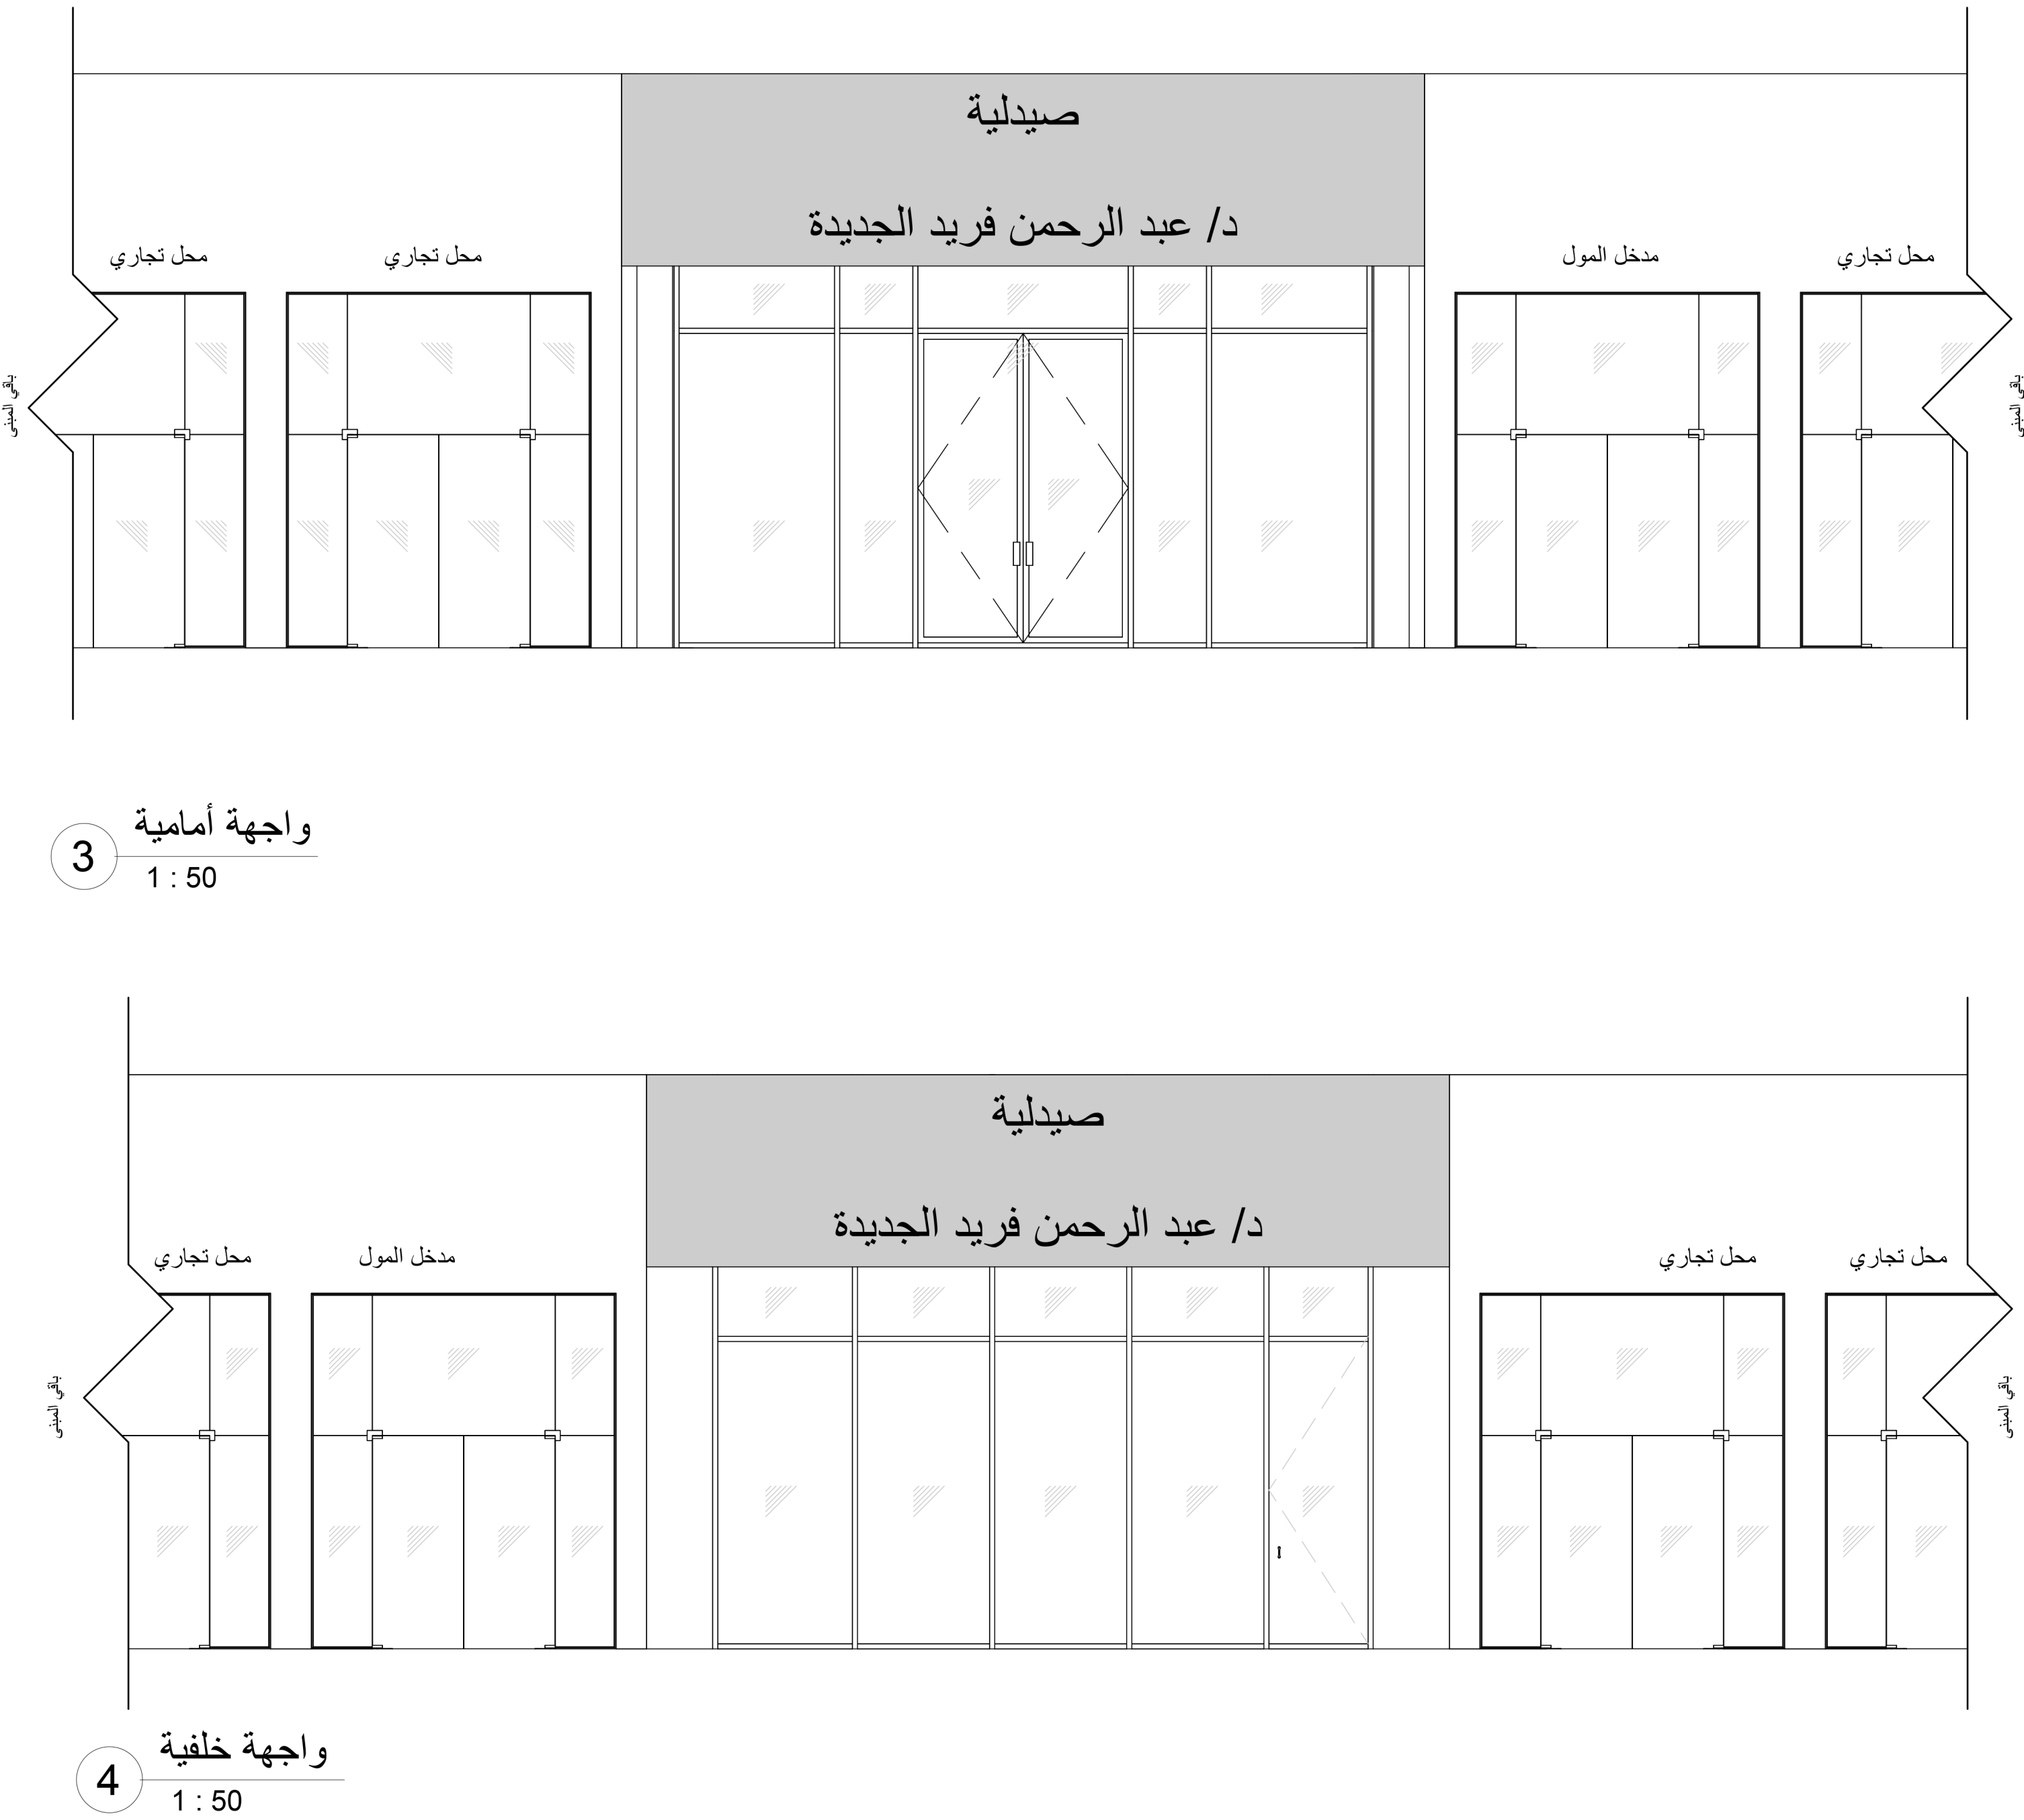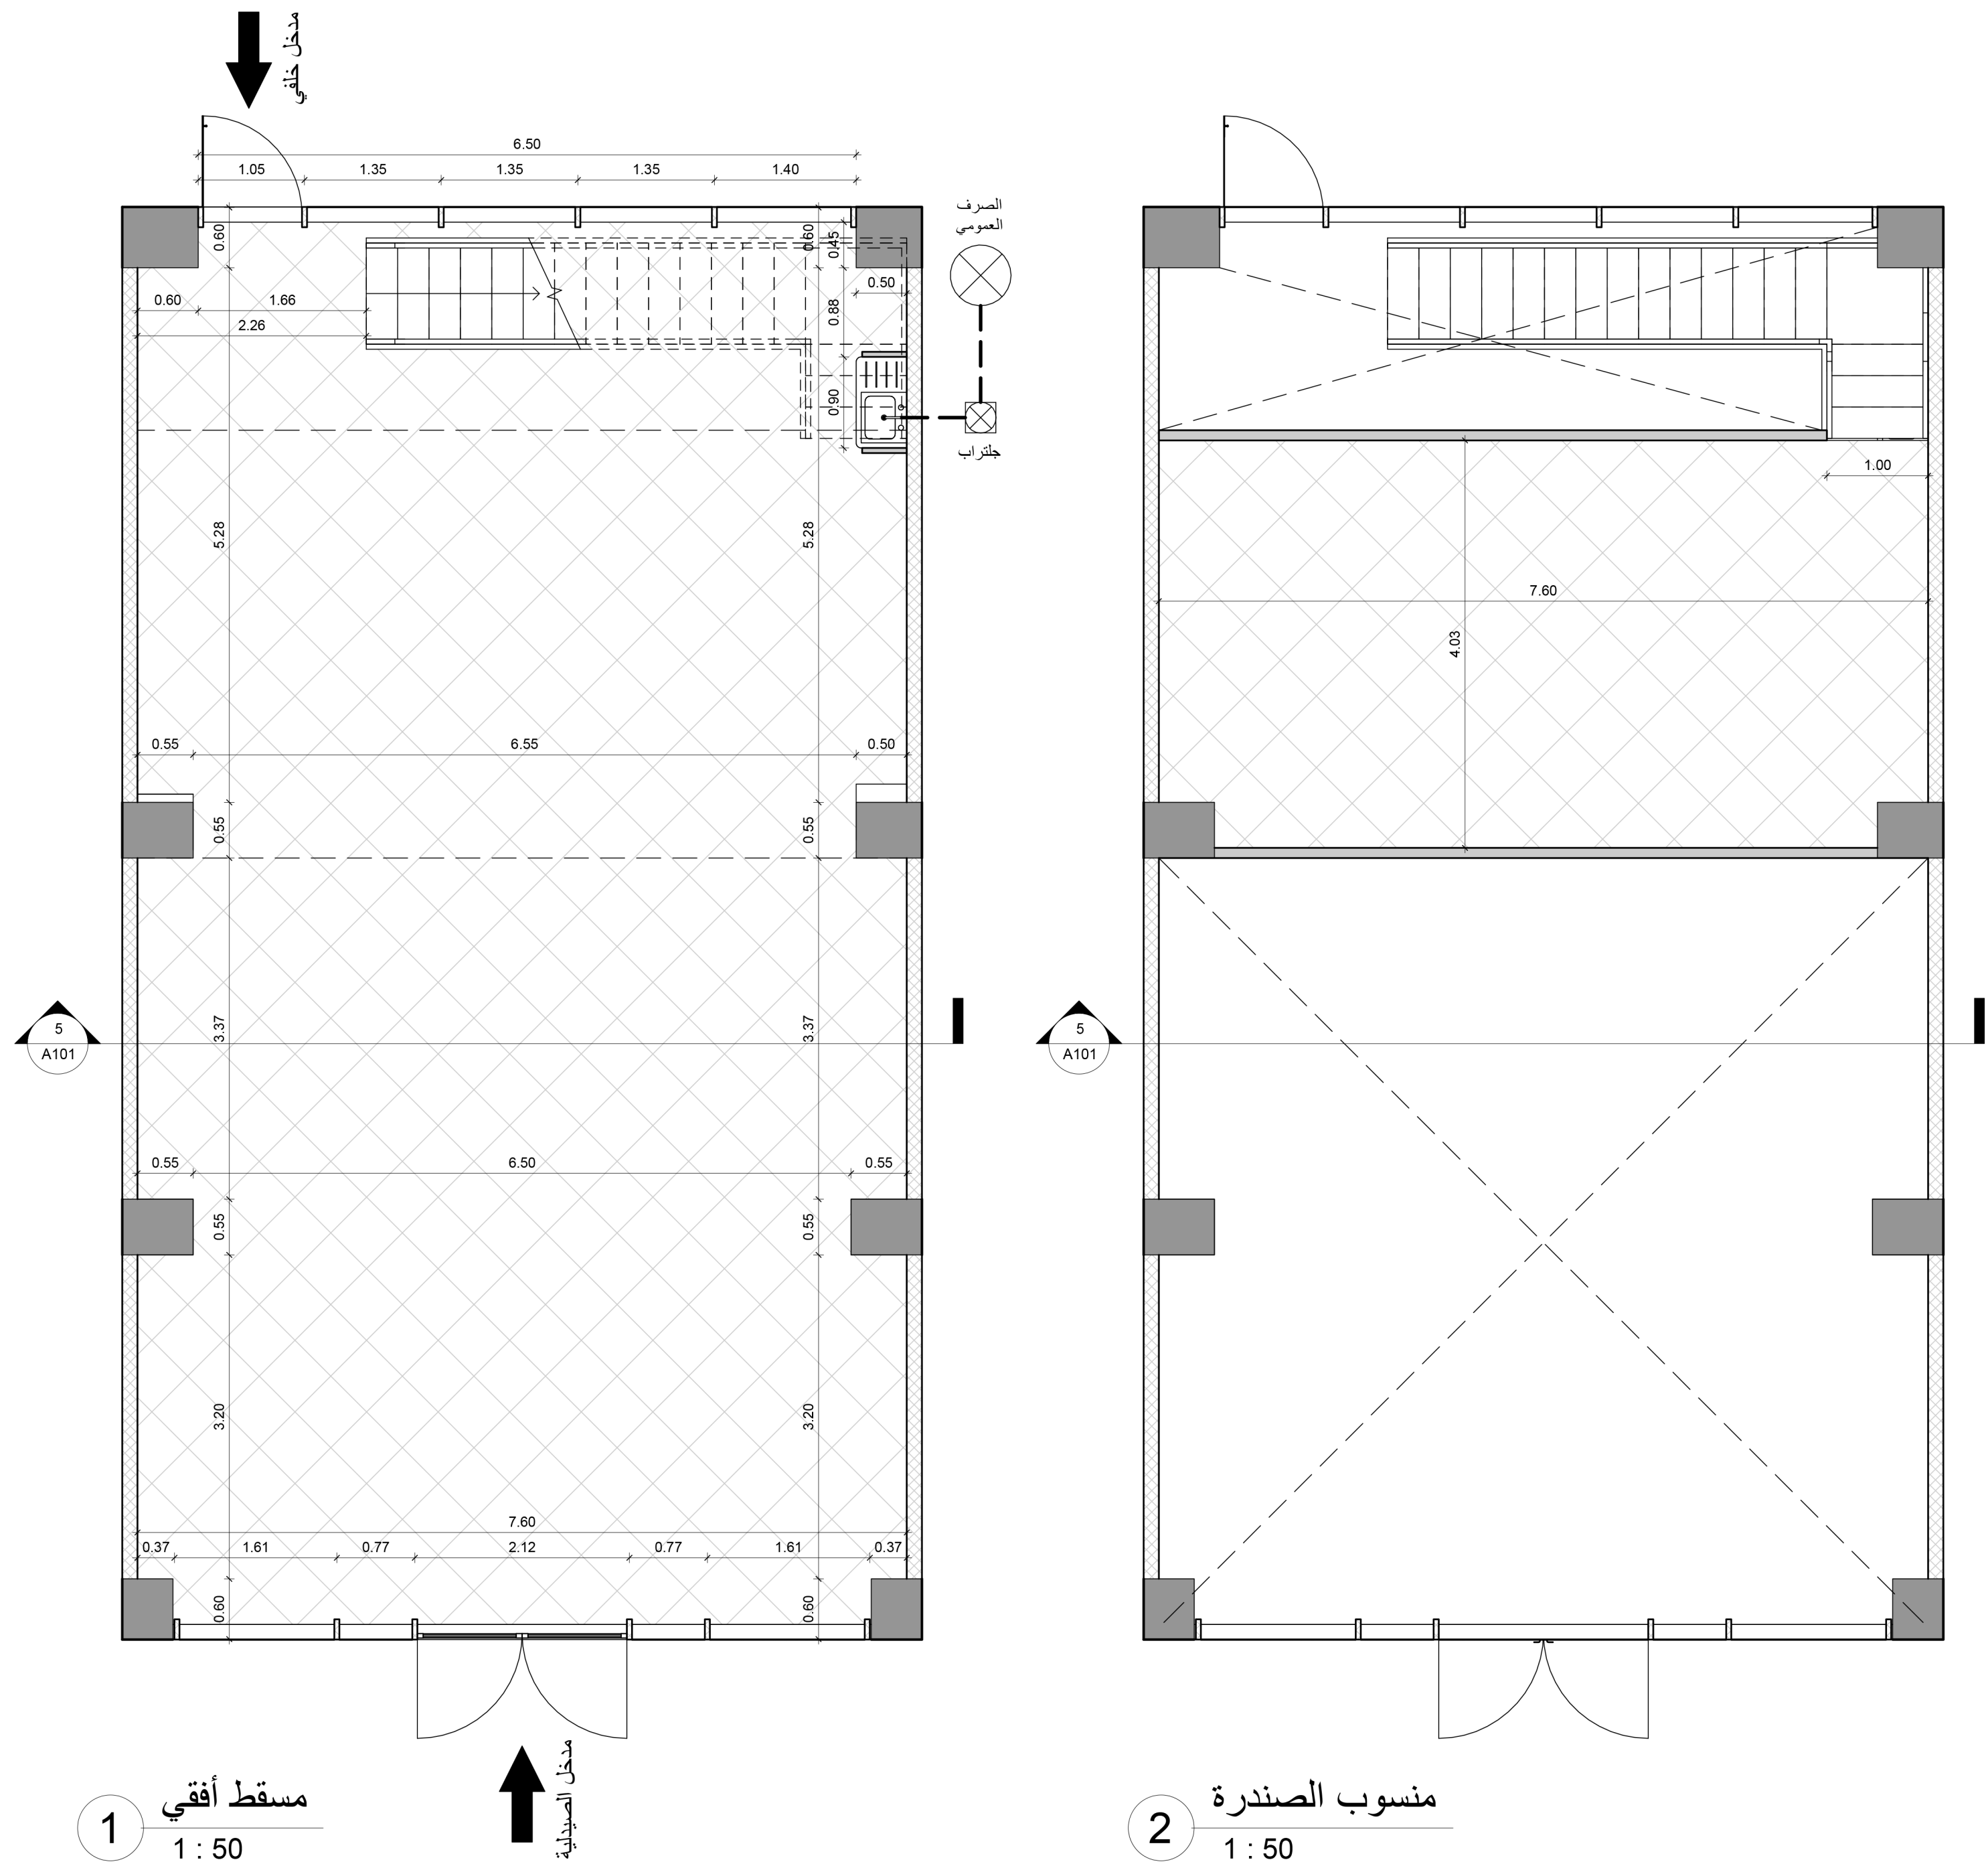


صاحب الصيدلية	صيدلية د/ عبد الرحمن فريد الجديدة
اسم الصيدلية	صيدلية د/ عبد الرحمن فريد الجديدة
المساحة	104.50 م2
العنوان	
مقياس الرسم	50:1
	
www.emocrete.com 01014490054	

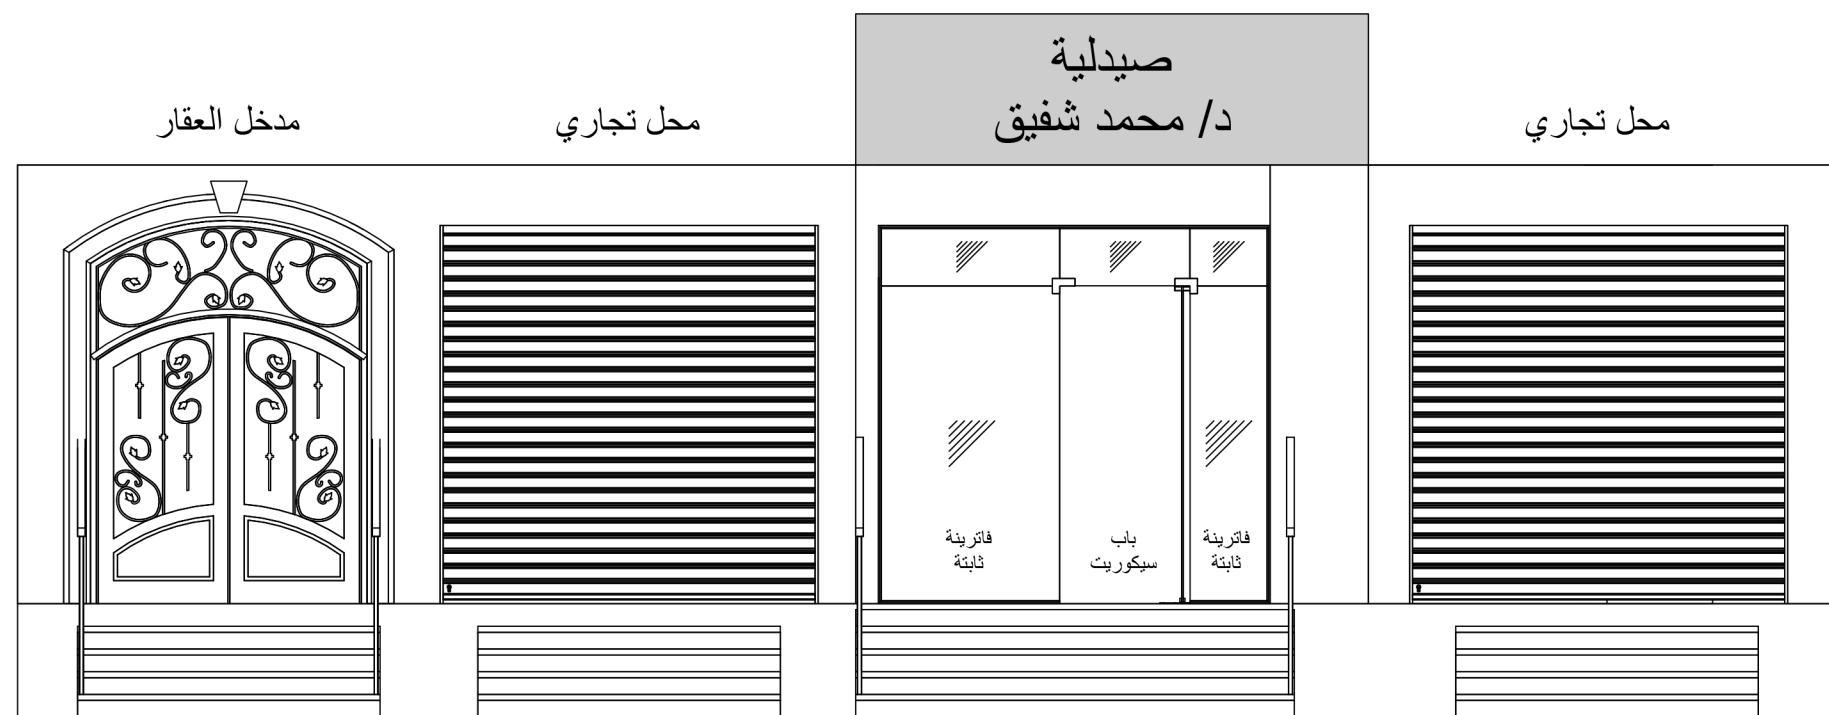


2 واجهة أمامية
1 : 50

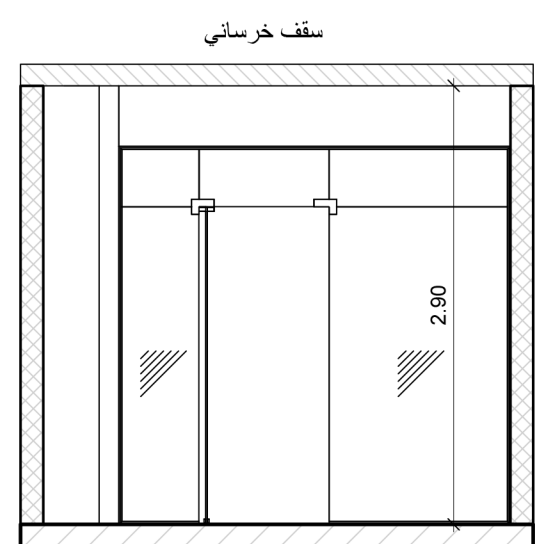

3 قطاع رأسي
1 : 50

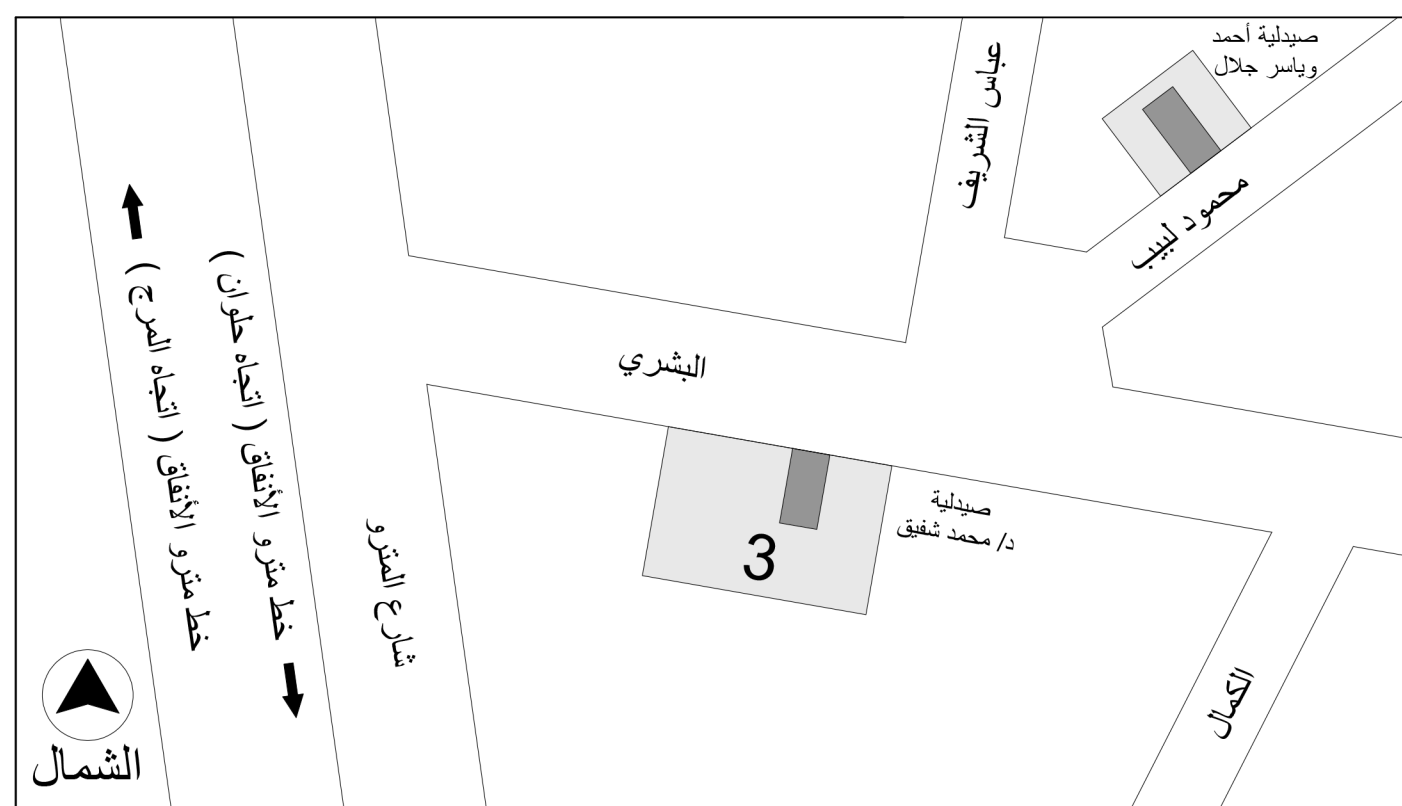


4 الموقع العام
1 : 1000

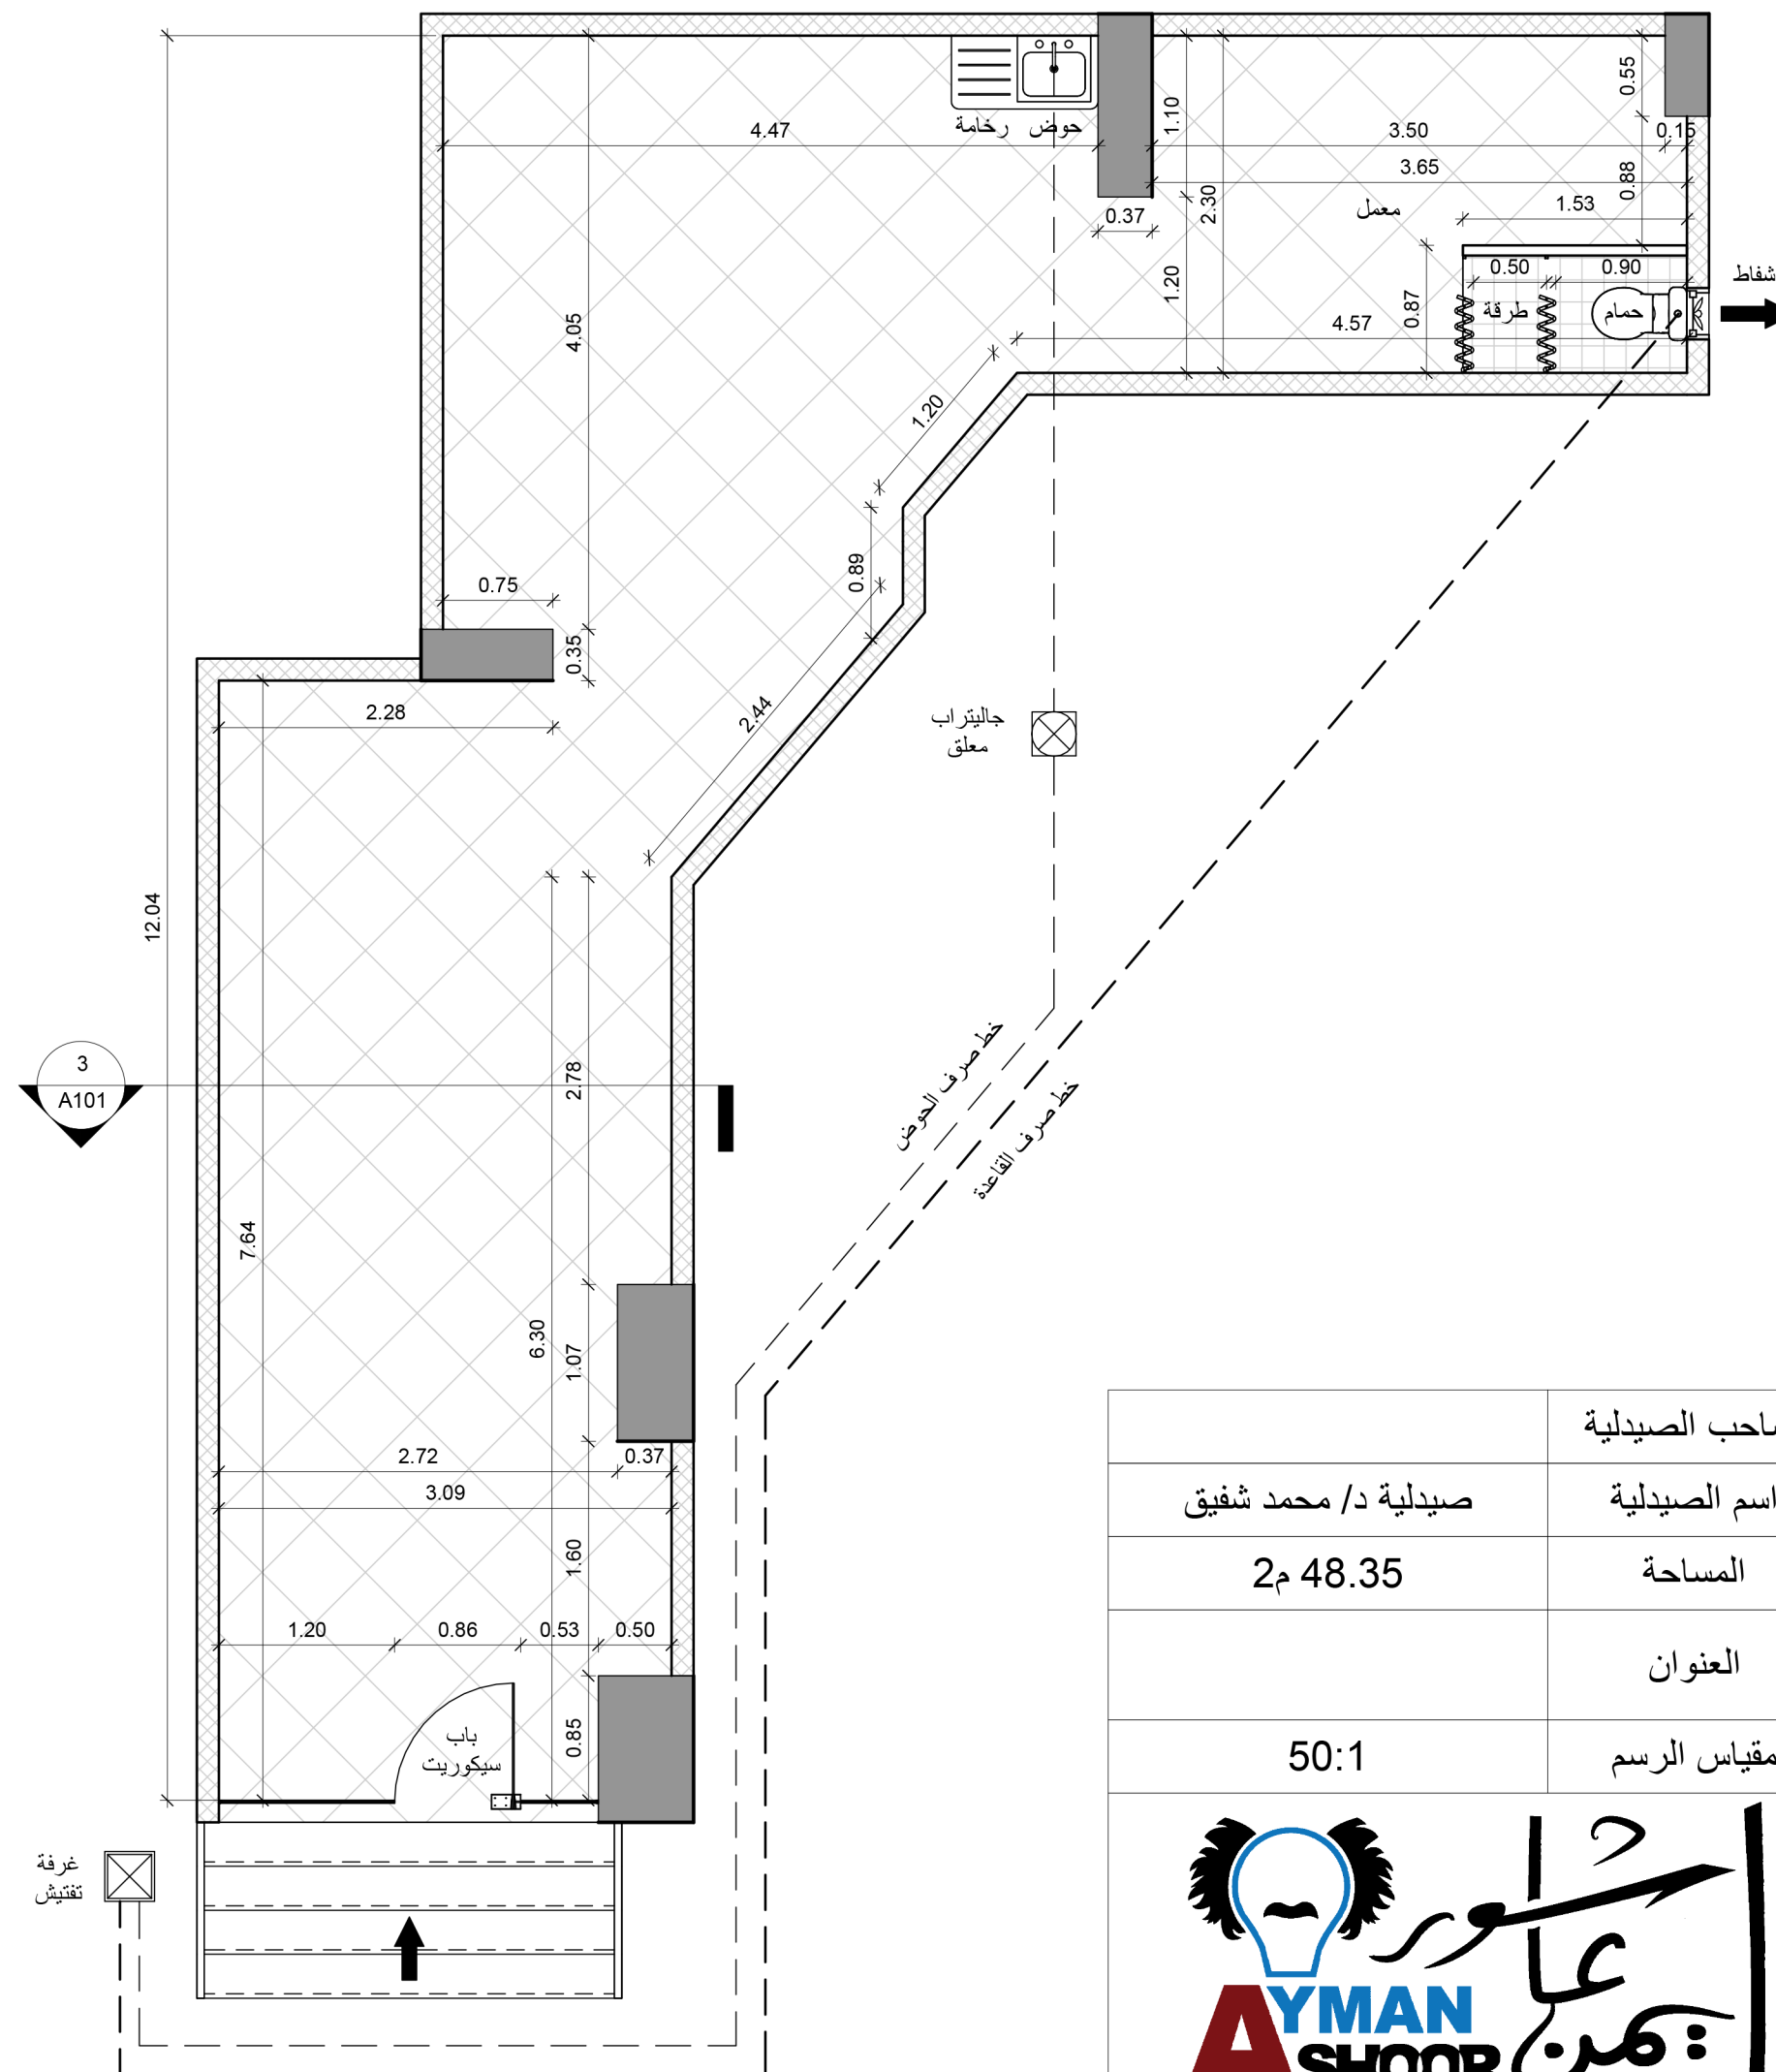



1 مسقط أفقي
1 : 50

صاحب الصيدلية	صيدلية د/ محمد شفيق
اسم الصيدلية	48.35 م ²
المساحة	50:1
العنوان	
مقياس الرسم	
www.emocrete.com 01014490054	

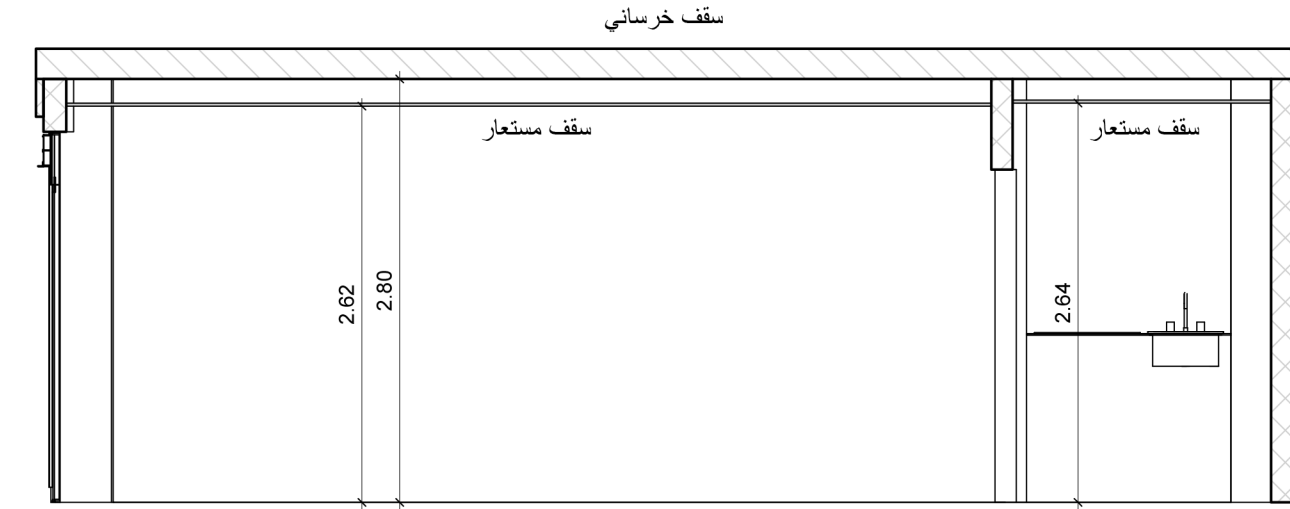

2 واجهة أمامية
1 : 50


5 قطاع رأسي
1 : 50

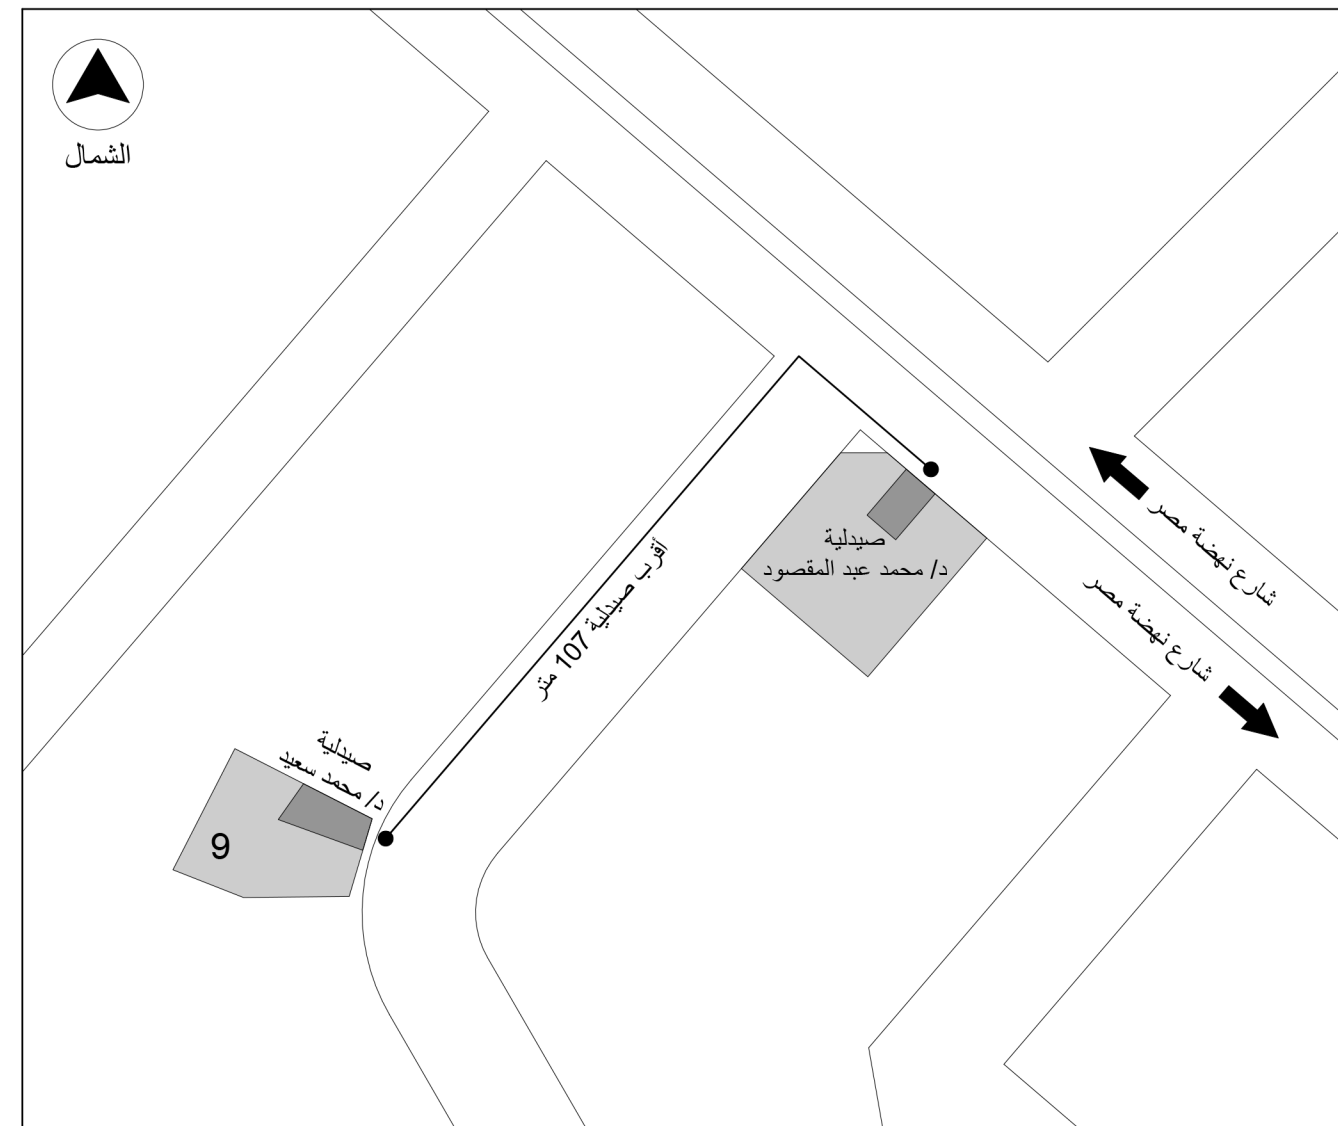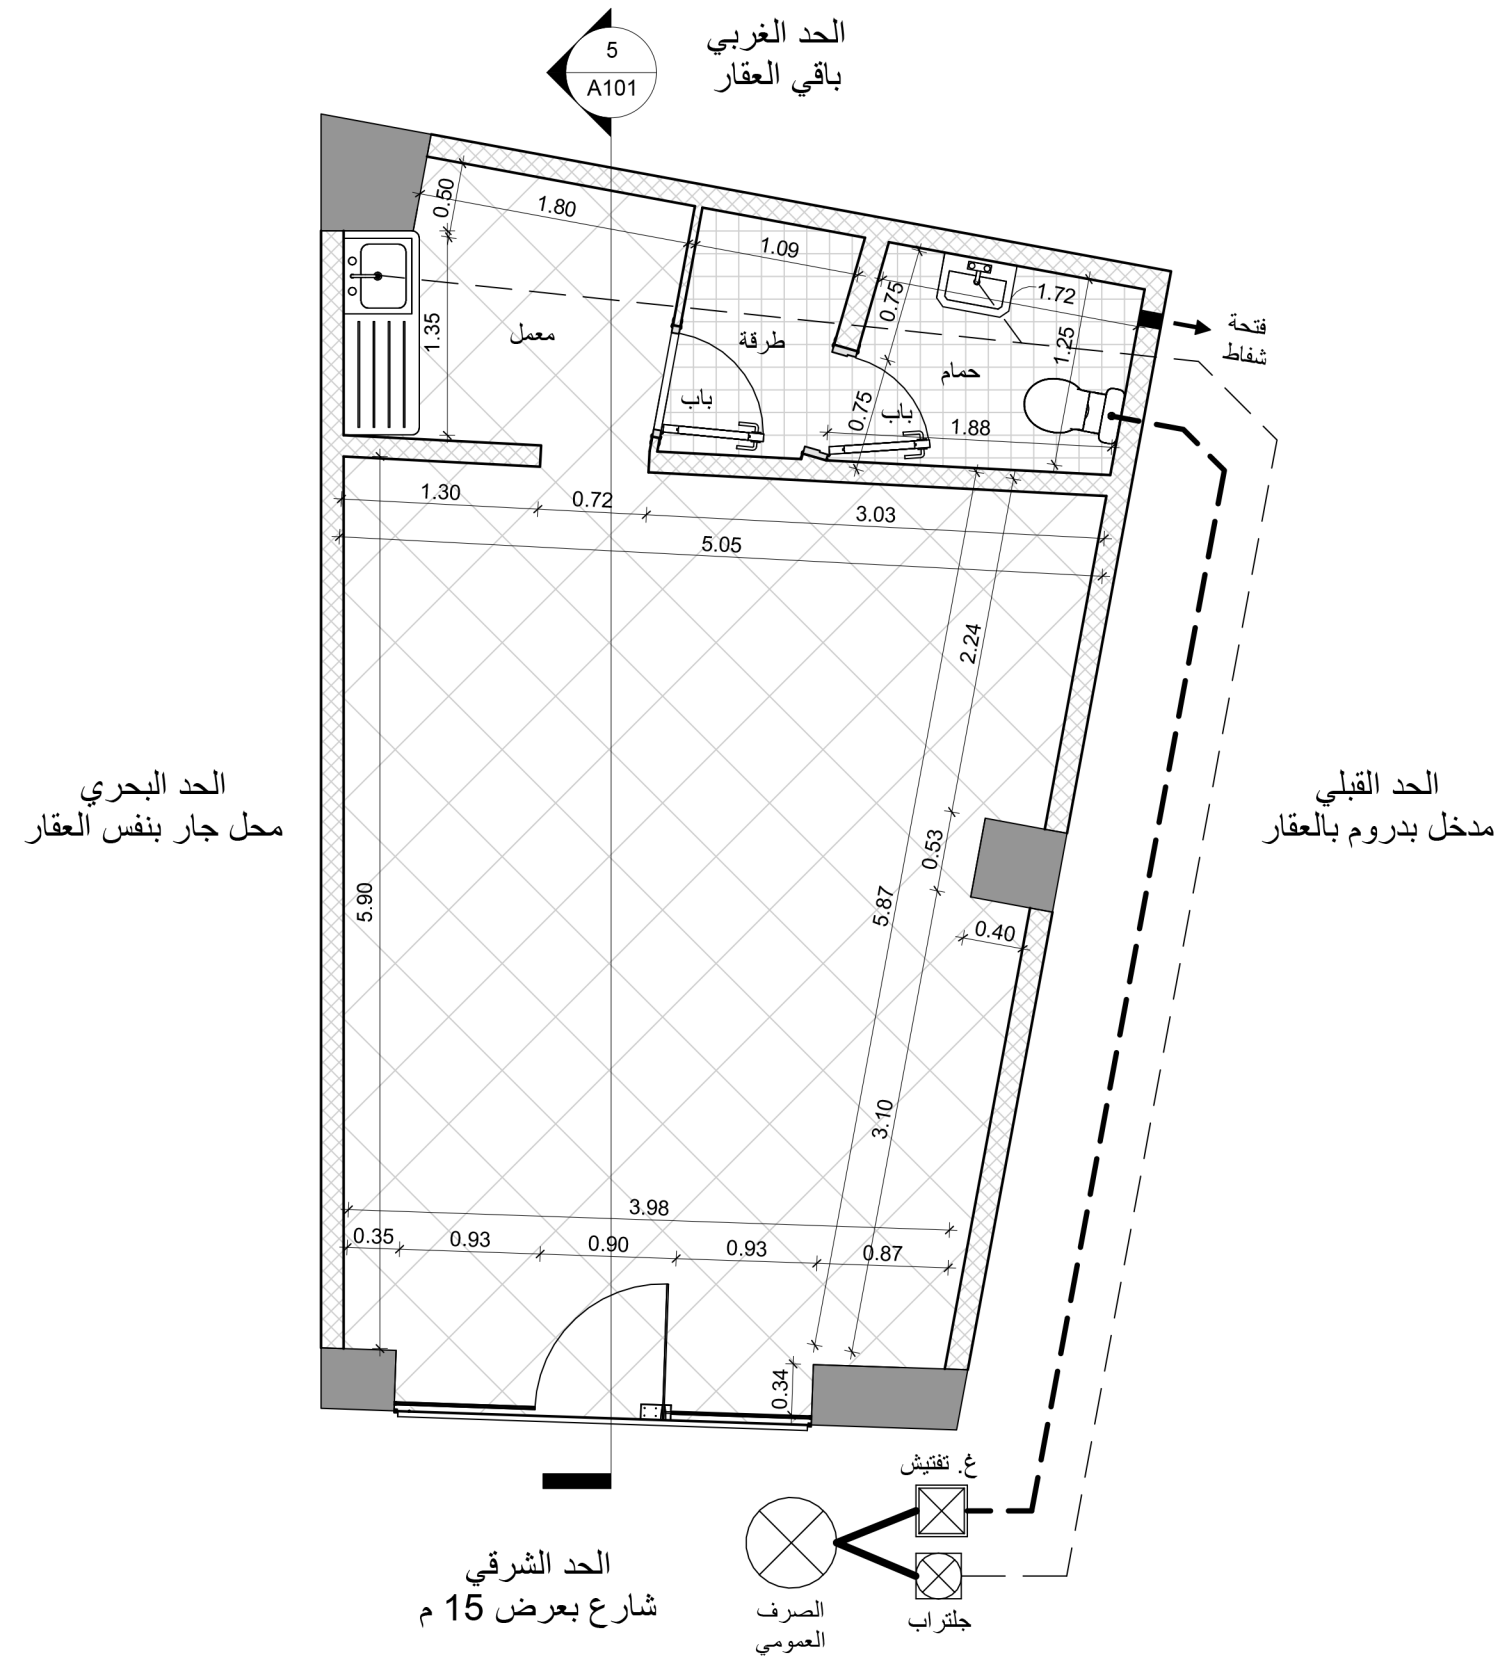


1 مسقط أفقي
1 : 50

4 الموقع العام
1 : 1000


صاحب الصيدلية	صيدلية محمد سعيد الجديدة
اسم الصيدلية	35.20 م2
المساحة	
العنوان	
مقياس الرسم	50:1
	
www.emocrete.com 01014490054	

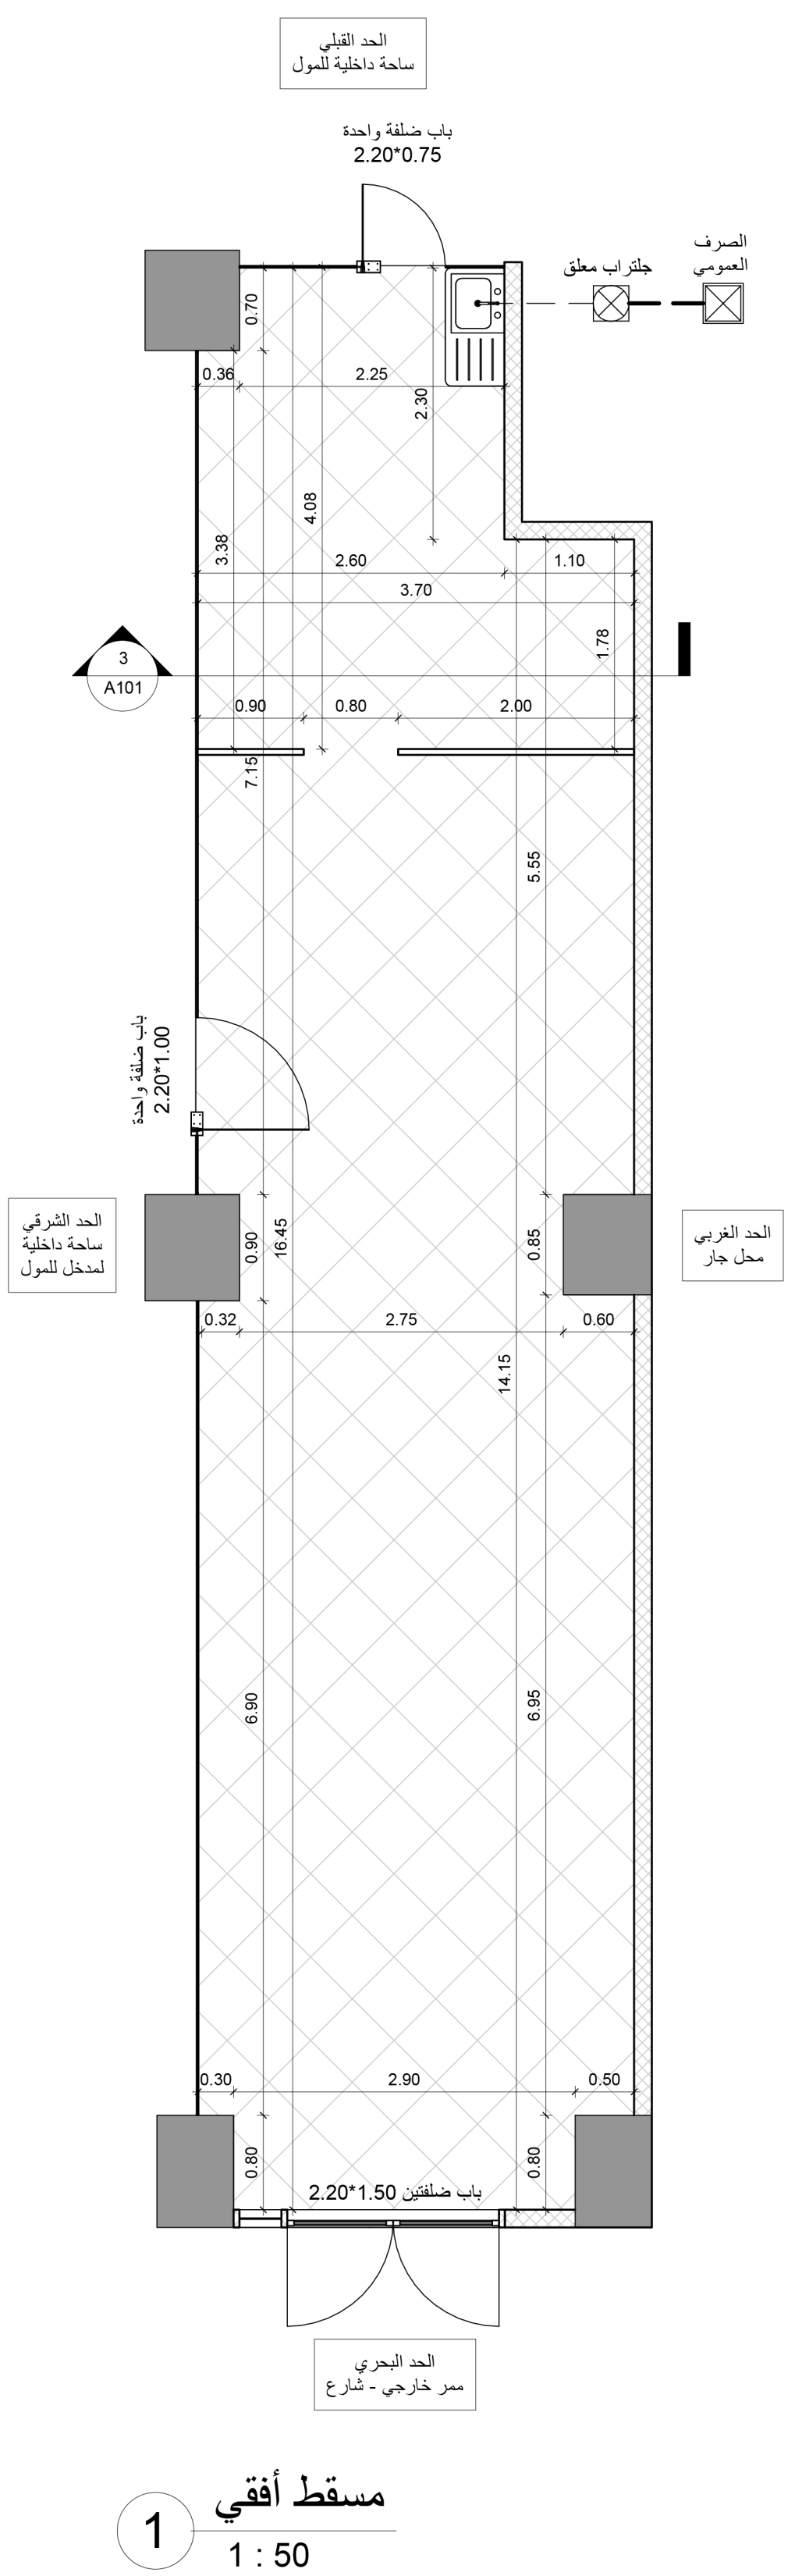


1
مستط أفقي
1 : 50

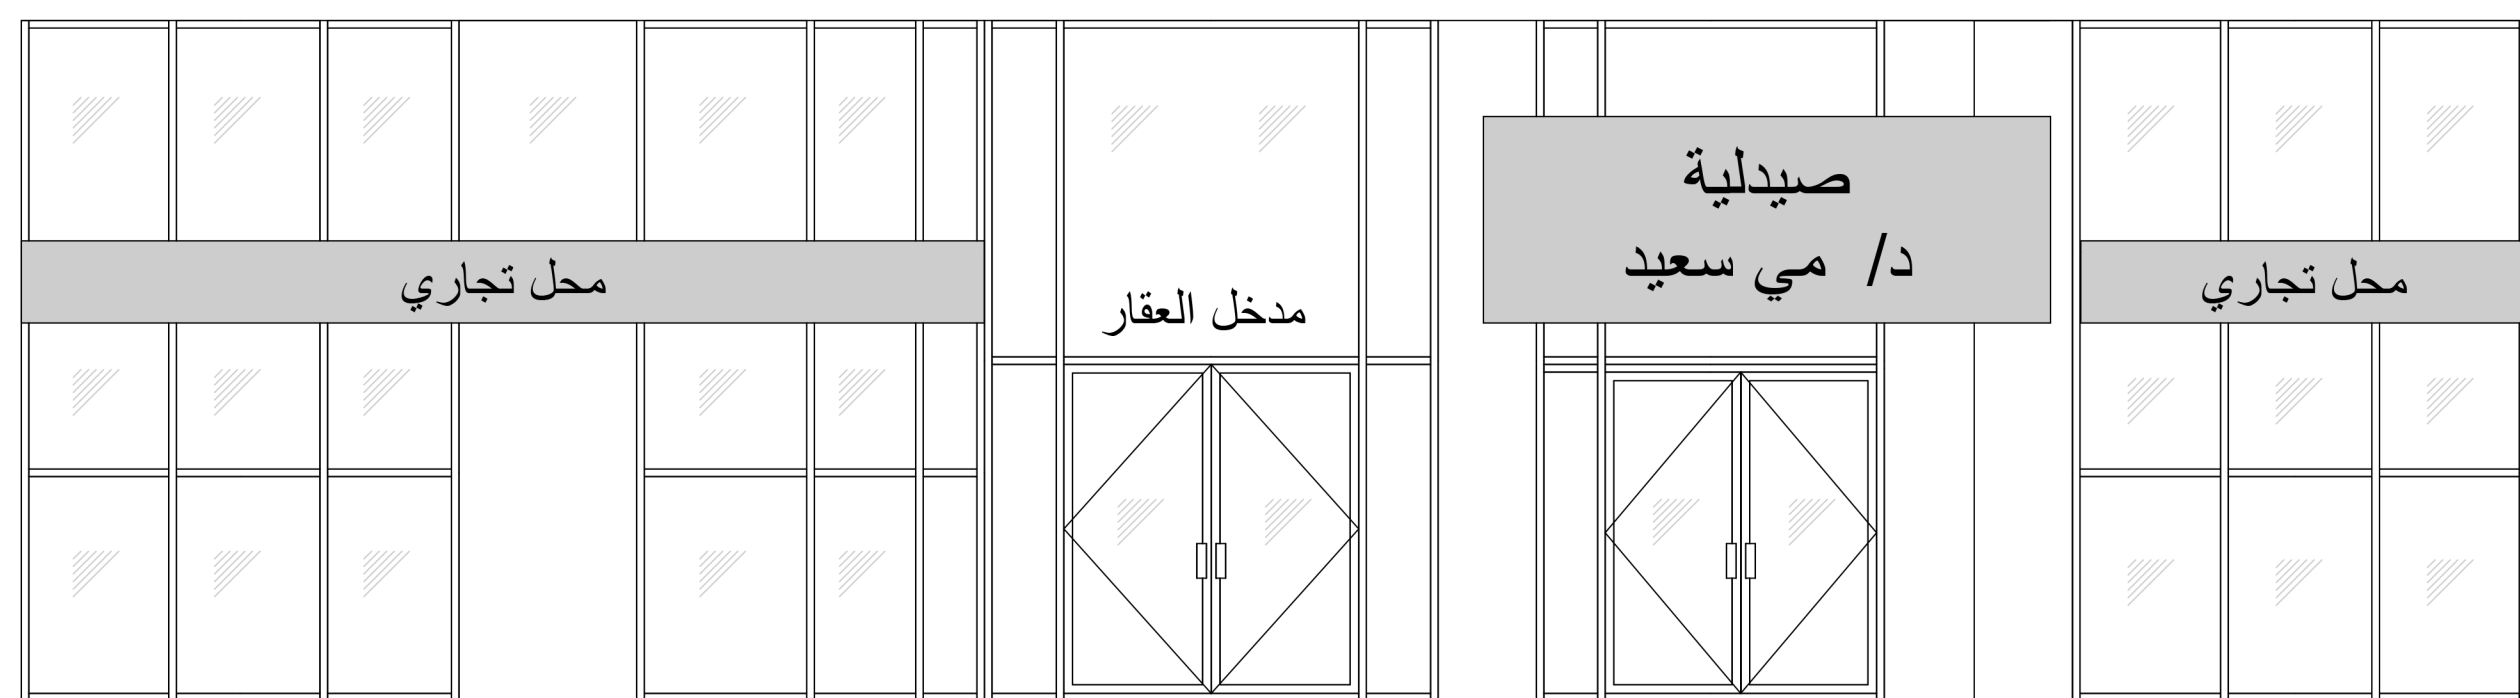


2
واجهة أمامية
1 : 50

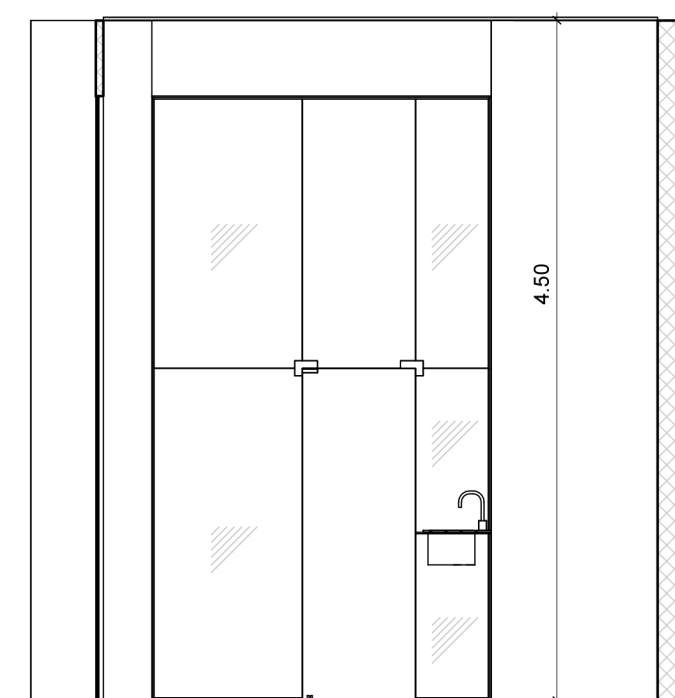


3
قطاع رأسي
1 : 50

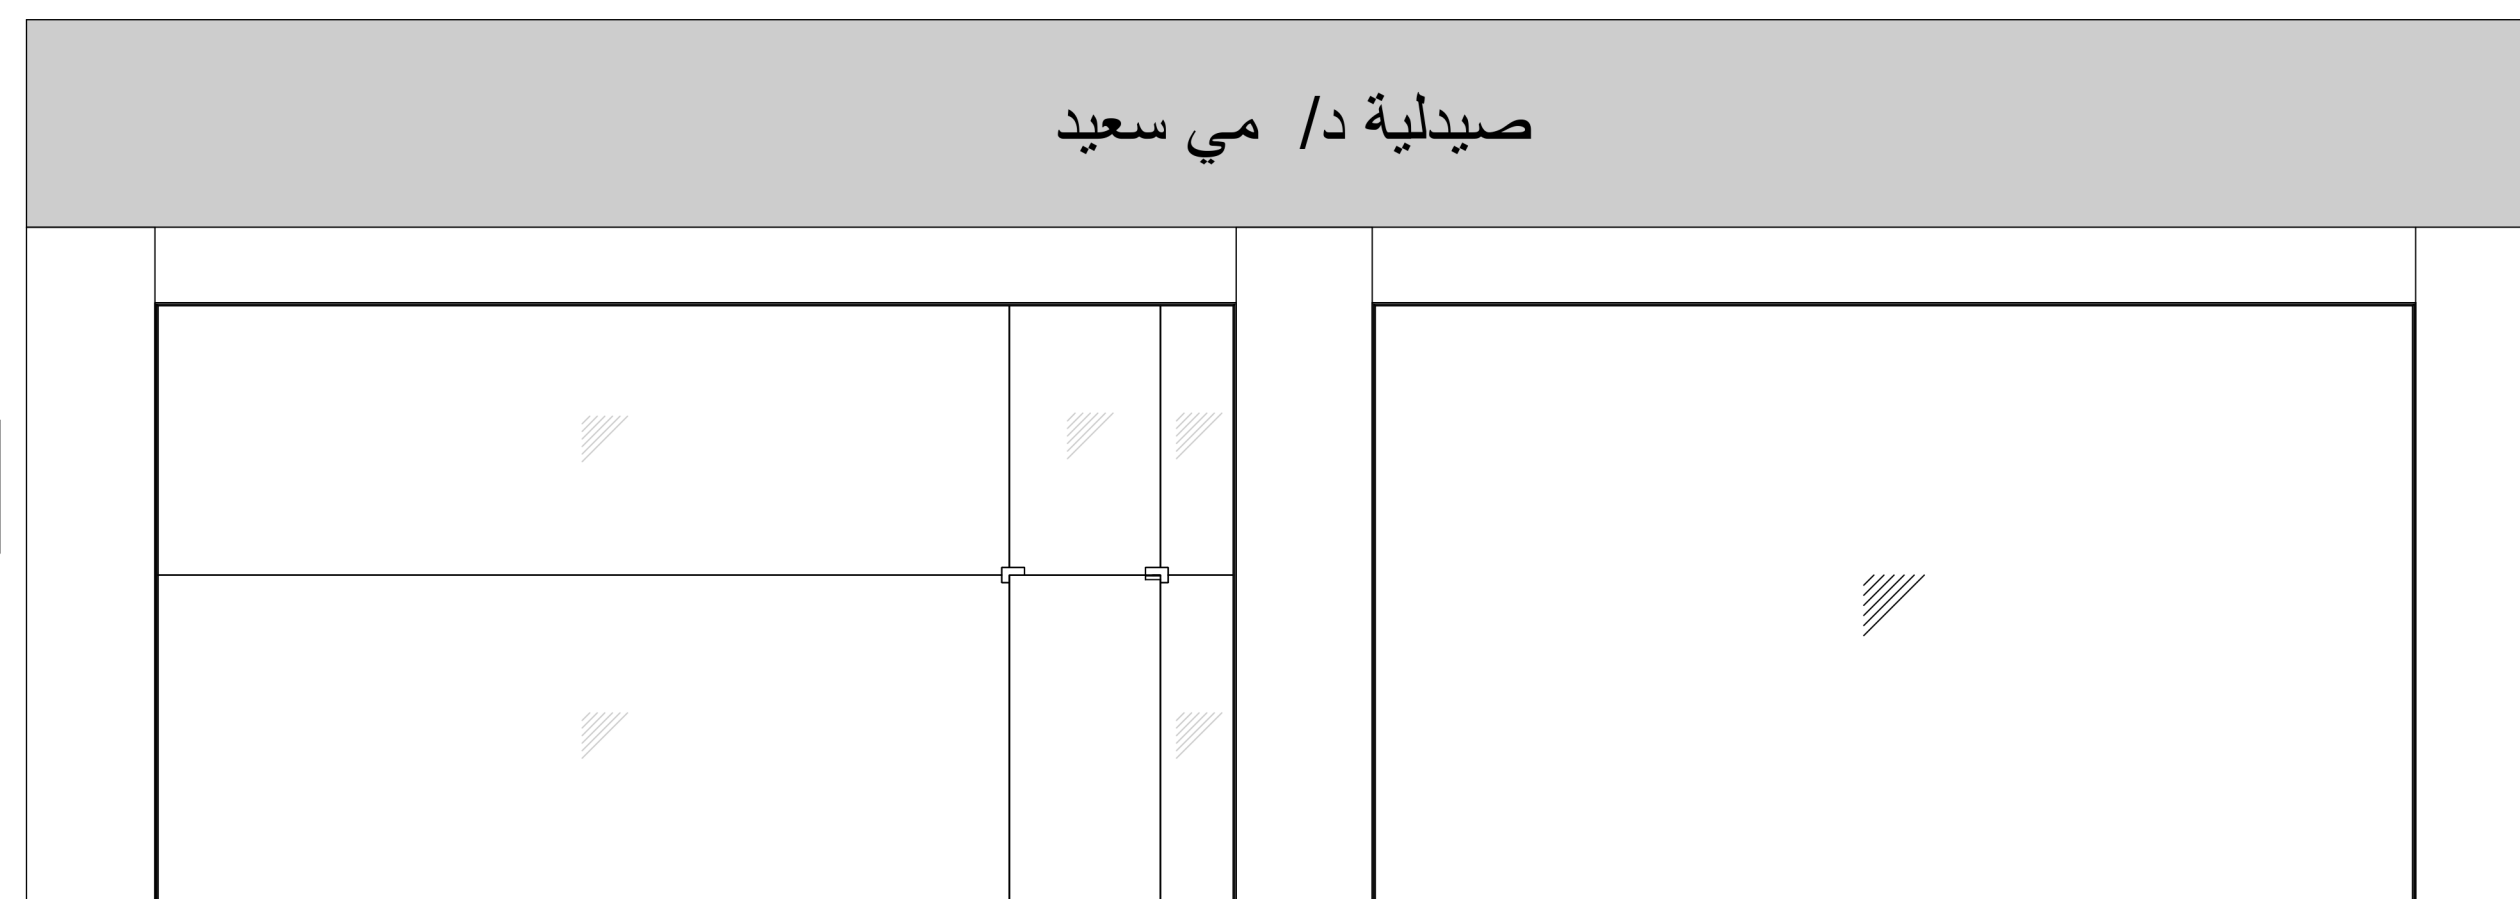

4
واجهة جانبية
1 : 50



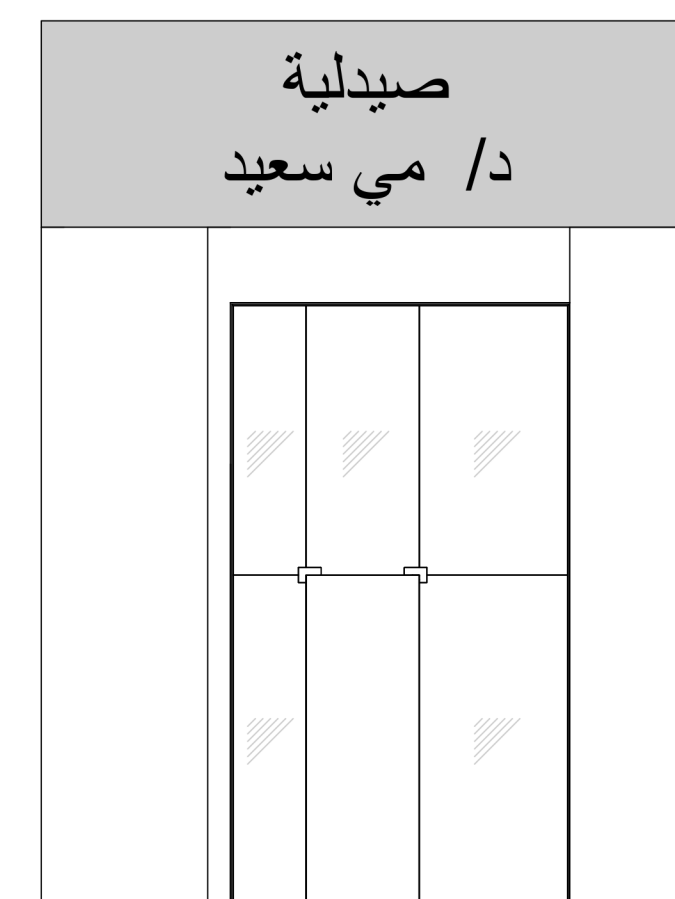


5
واجهة خلفية
1 : 50

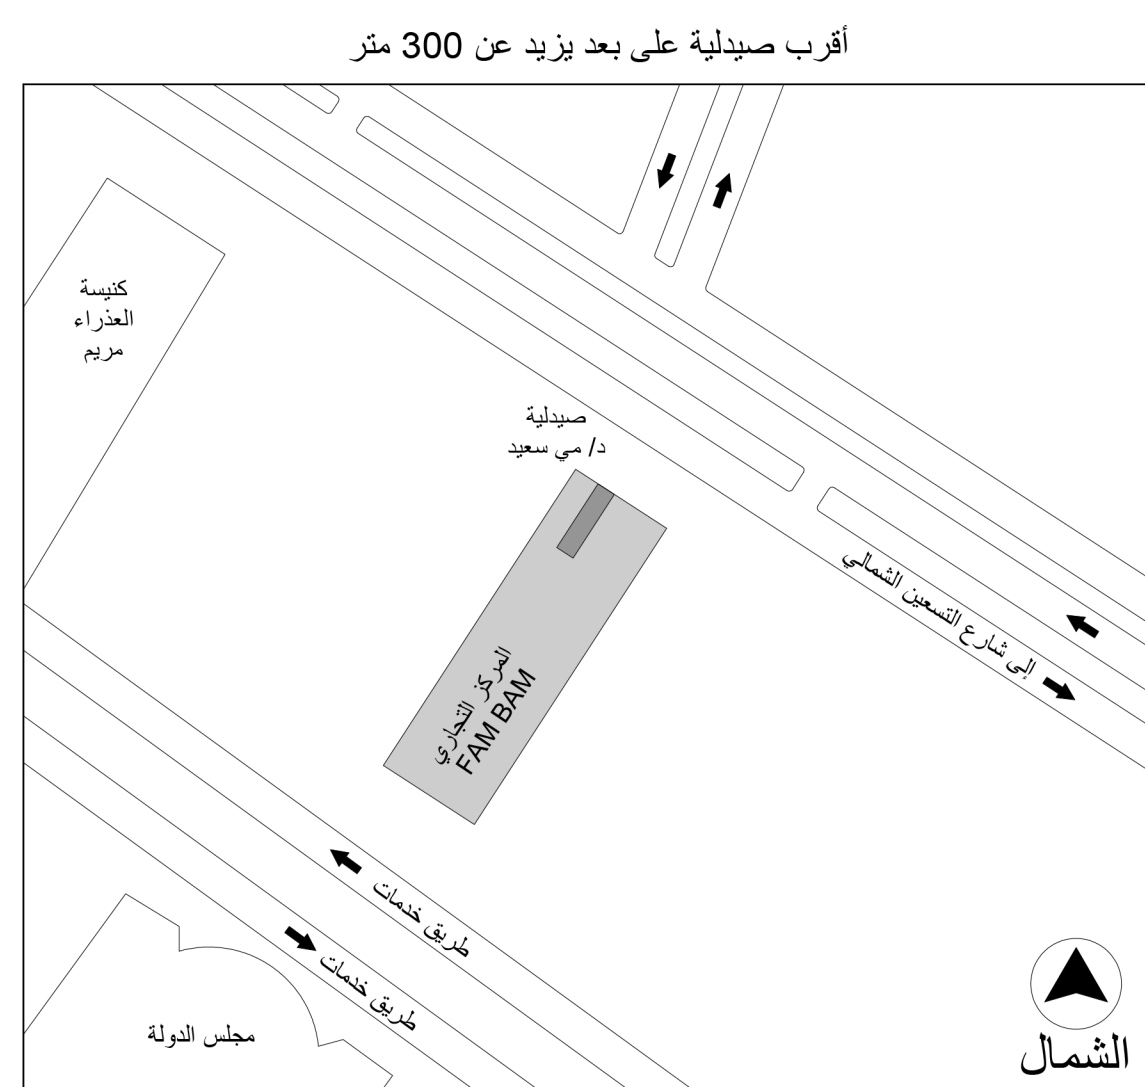

6
الموقع العام
1 : 2000

صاحب الصيدلية	صيدلية د/ مي سعيد
اسم الصيدلية	صيدلية د/ مي سعيد
المساحة	58.34 م ²
العنوان	
مقياس الرسم	50:1
www.emocrete.com 01014490054	

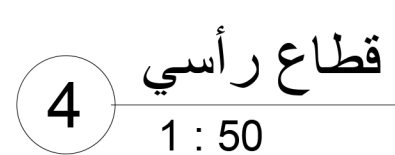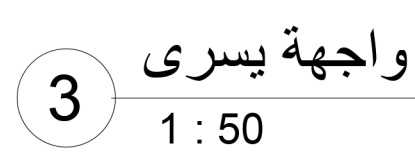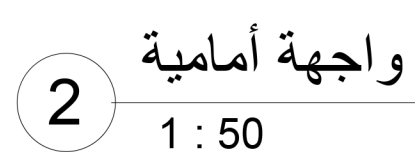

صاحب الصيدلية	
اسم الصيدلية	صيدلية د/ وائل طه
المساحة	2م 46.40
العنوان	
مقياس الرسم	50:1
	
www.emocrete.com 01014490054	